


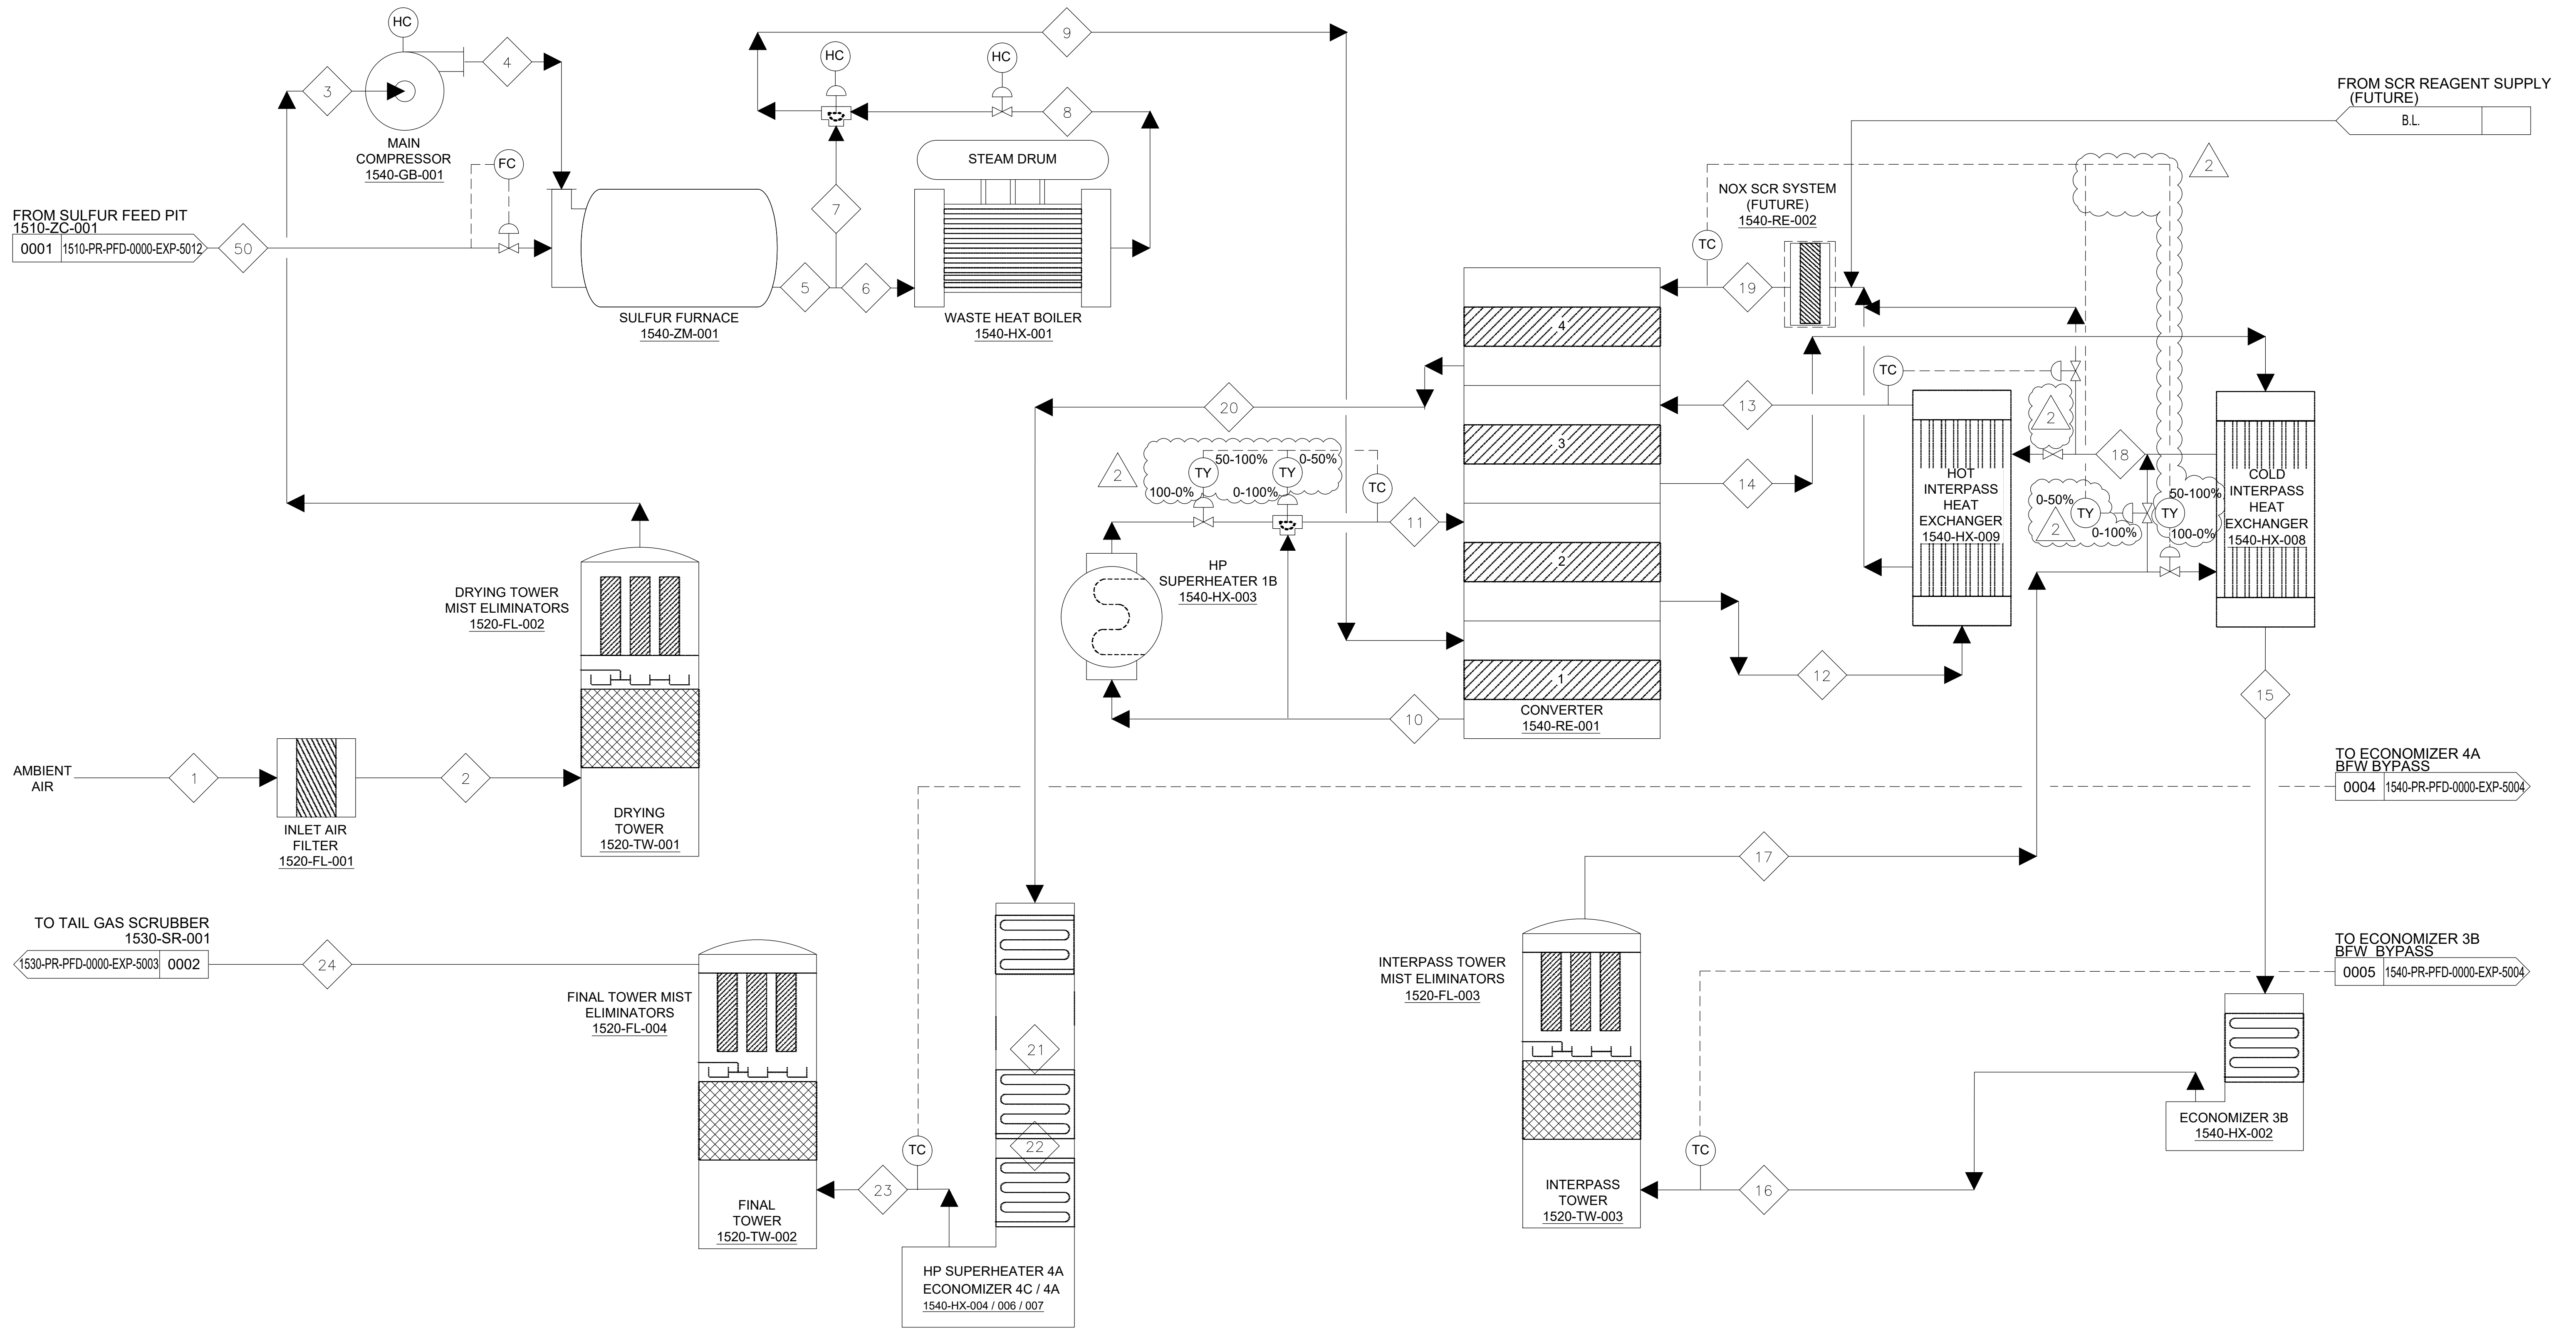

1500-PR-HMB-0000-EXP-5007	MATERIAL BALANCE DESIGN CASE 105 RATE CLEAN
1500-PR-HMB-0000-EXP-5006	MATERIAL BALANCE DESIGN CASE DIRTY
DWG. NO.	TITLE
REFERENCES	

NOTES:

2	REVISED CONTROL REPRESENTATION				2024-09-23
1	HRS TOWER REPLACED BY INTERPASS TOWER	SJ	BA	TV	2024-08-01
0	ISSUED FOR DESIGN	RM	BA	TV	2024-01-16
B	ISSUED FOR CLIENT REVIEW	RM	BA	TV	2023-12-11
A	ISSUED FOR REVIEW	RM	BA		2023-11-23
NO.	DESCRIPTION	BY	CHK	APP'D	DATE
REVISIONS					

SEAL

EXP

t: +1.713.439.3600 | f: +1.713.963.9085
exp.com

NOTICE

Property of Lithium Americas Corp (LAC). The contents of this drawing are confidential and proprietary to Lithium Americas Corp. The information contained in this drawing may not be distributed, duplicated, or modified without prior written permission from Lithium Americas Corp. All rights reserved

SCALE	SIZE
N/A	D
DRAWN BY	DATE
R. MASANI	2024-01-16
CHECKED BY	DATE
D. BIRD	2024-01-16
ENGINEERED BY	DATE
B. AFELSKIE	2024-01-16
APPROVED BY	DATE
T. VAN DAELE	2024-01-16


LithiumAmericas

TITLE

2,250MTPD SA1 - DCDA
PROCESS FLOW DIAGRAM
GAS

THACKER PASS PROJECT HUMBOLDT COUNTY, NV	
PROJ No. HOU-23001048-A1	REV
DRAWING No.	
1540-PR-PFD-0000-EXP-5001	2

DRAWING PLOTTED:

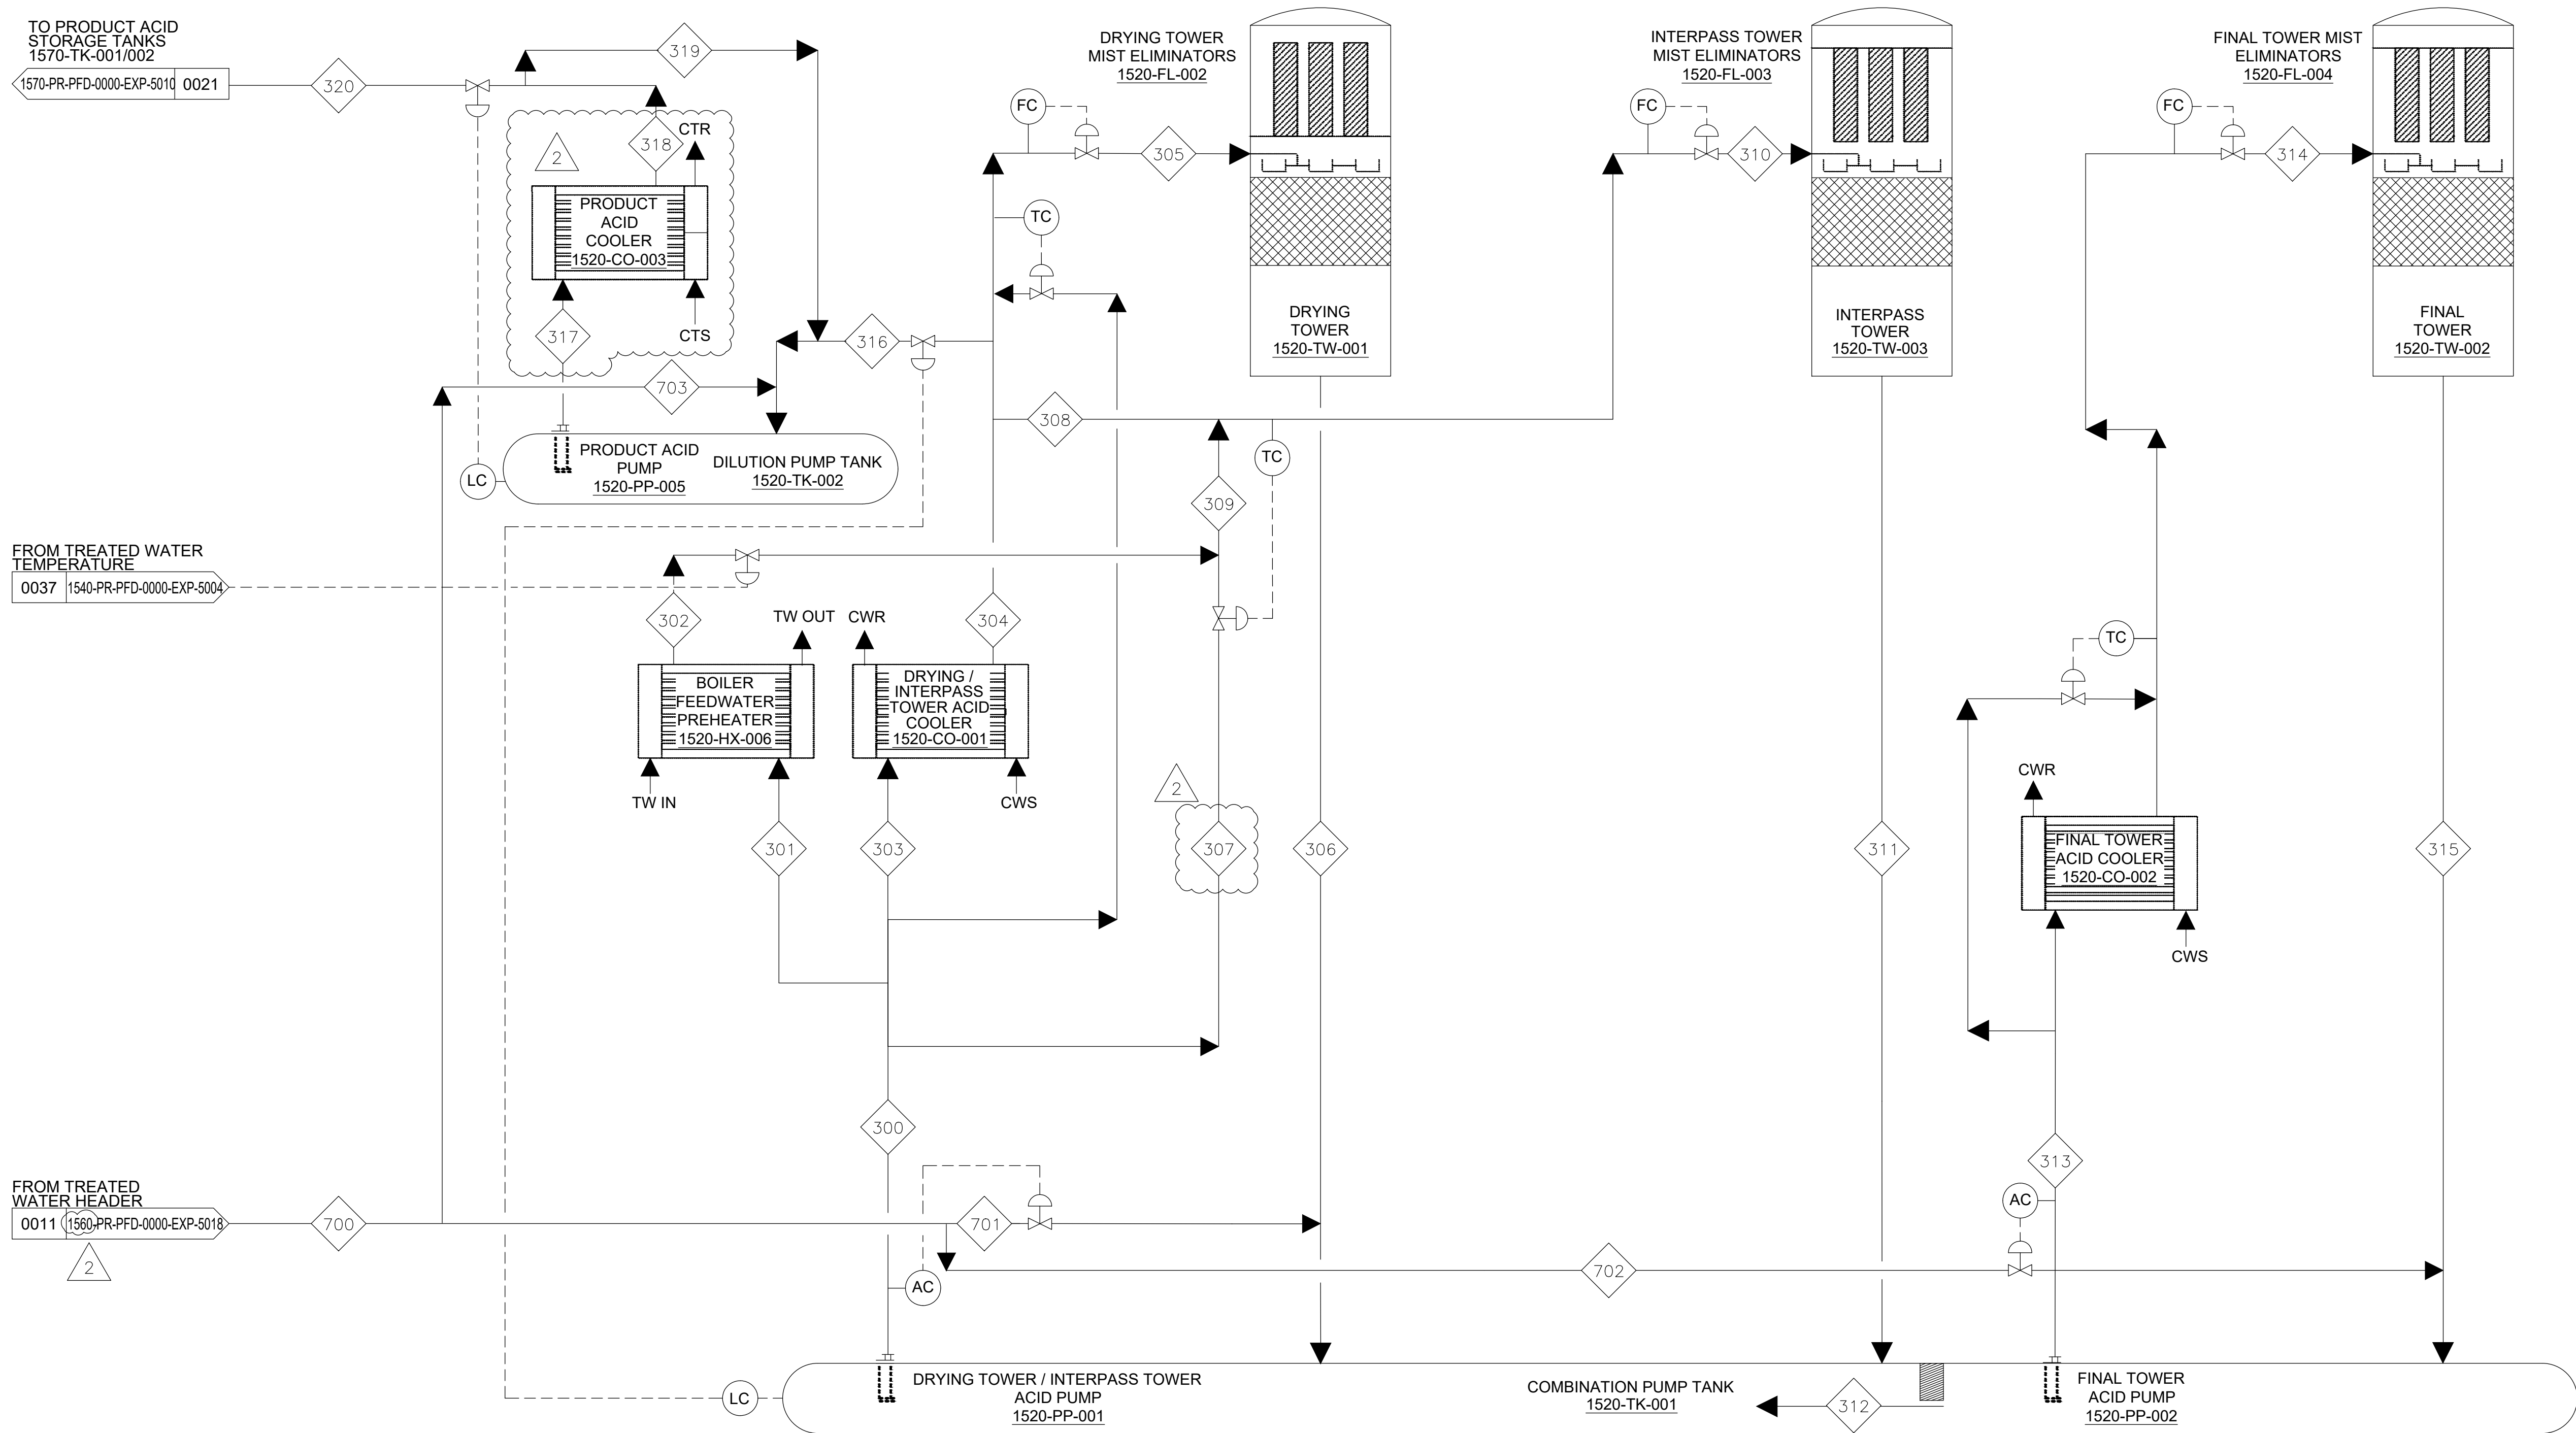

1500-PR-HMB-0000-EXP-5007	MATERIAL BALANCE DESIGN 105 RATE CLEAN
1500-PR-HMB-0000-EXP-5006	MATERIAL BALANCE DESIGN CASE DIRTY
DWG. NO.	TITLE
REFERENCES	

NOTES:	

2	REVISED PRODUCT COOLER REPRESENTATION				2024-09-23
1	RECONFIGURED FROM HRS READY TO DCDA	SJ	BA	TV	2024-08-01
0	ISSUED FOR DESIGN	RM	BA	TV	2024-01-16
B	ISSUED FOR CLIENT REVIEW	RM	BA	TV	2023-12-11
A	ISSUED FOR REVIEW	RM	BA		2023-11-23
NO.	DESCRIPTION	BY	CHK	APP'D	DATE
REVISIONS					

SEAL
EXP
EXP
EXP

NOTICE
Property of Lithium Americas Corp (LAC). The contents of this drawing are confidential and proprietary to Lithium Americas Corp. The information contained in this drawing may not be distributed, duplicated, or modified without prior written permission from Lithium Americas Corp. All rights reserved.

SCALE	N/A	SIZE	D
DRAWN BY	R. MASANI	DATE	2024-01-16
CHECKED BY	D. BIRD	DATE	2024-01-16
ENGINEERED BY	B. AFELSKIE	DATE	2024-01-16
APPROVED BY	T. VAN DAELE	DATE	2024-01-16


TITLE	
2,250MTPD SA1 - DCDA PROCESS FLOW DIAGRAM STRONG ACID	

THACKER PASS PROJECT HUMBOLDT COUNTY, NV	
PROJ No. HOU-23001048-A1	REV
DRAWING No.	
1520-PR-PFD-0000-EXP-5002	2

PROPRIETARY AND CONFIDENTIAL

THE MASTER VERSION OF THIS DOCUMENT IS STORED AS A DIGITAL FILE IN A SOFTWARE ARCHIVE. THIS DOCUMENT IS PRODUCED BY EXP U.S. SERVICES INC. ("EXP") FOR THE LITHIUM NEVADA CORPORATION THACKER PASS SULFURIC ACID PLANT PROJECT ("PROJECT") WHICH IS BASED IN PART ON THE PROCESS DESIGN OF MECS, INC. ("MECS"). IT CONTAINS PROPRIETARY AND CONFIDENTIAL INFORMATION AND KNOW-HOW AND MAY INCLUDE PATENTED INTELLECTUAL PROPERTY THAT ARE, IN EACH CASE, PROPERTY OF MECS OR EXP (TOGETHER, THE "CONTRACTORS") AND AS SUCH SHALL NOT BE USED, DISCLOSED, DISSEMINATED, PUBLISHED, OR REPRODUCED, IN WHOLE OR IN PART, FOR ANY PURPOSE OTHER THAN FOR WHICH IT WAS SUPPLIED BY EXP, EXCEPT IN ACCORDANCE TO THE TERMS OF THE CONTRACT(S) ENTERED INTO WITH RESPECT TO THE PROJECT OR WITH WRITTEN PERMISSION OF THE CONTRACTORS.*

DRAWING PLOTTED:

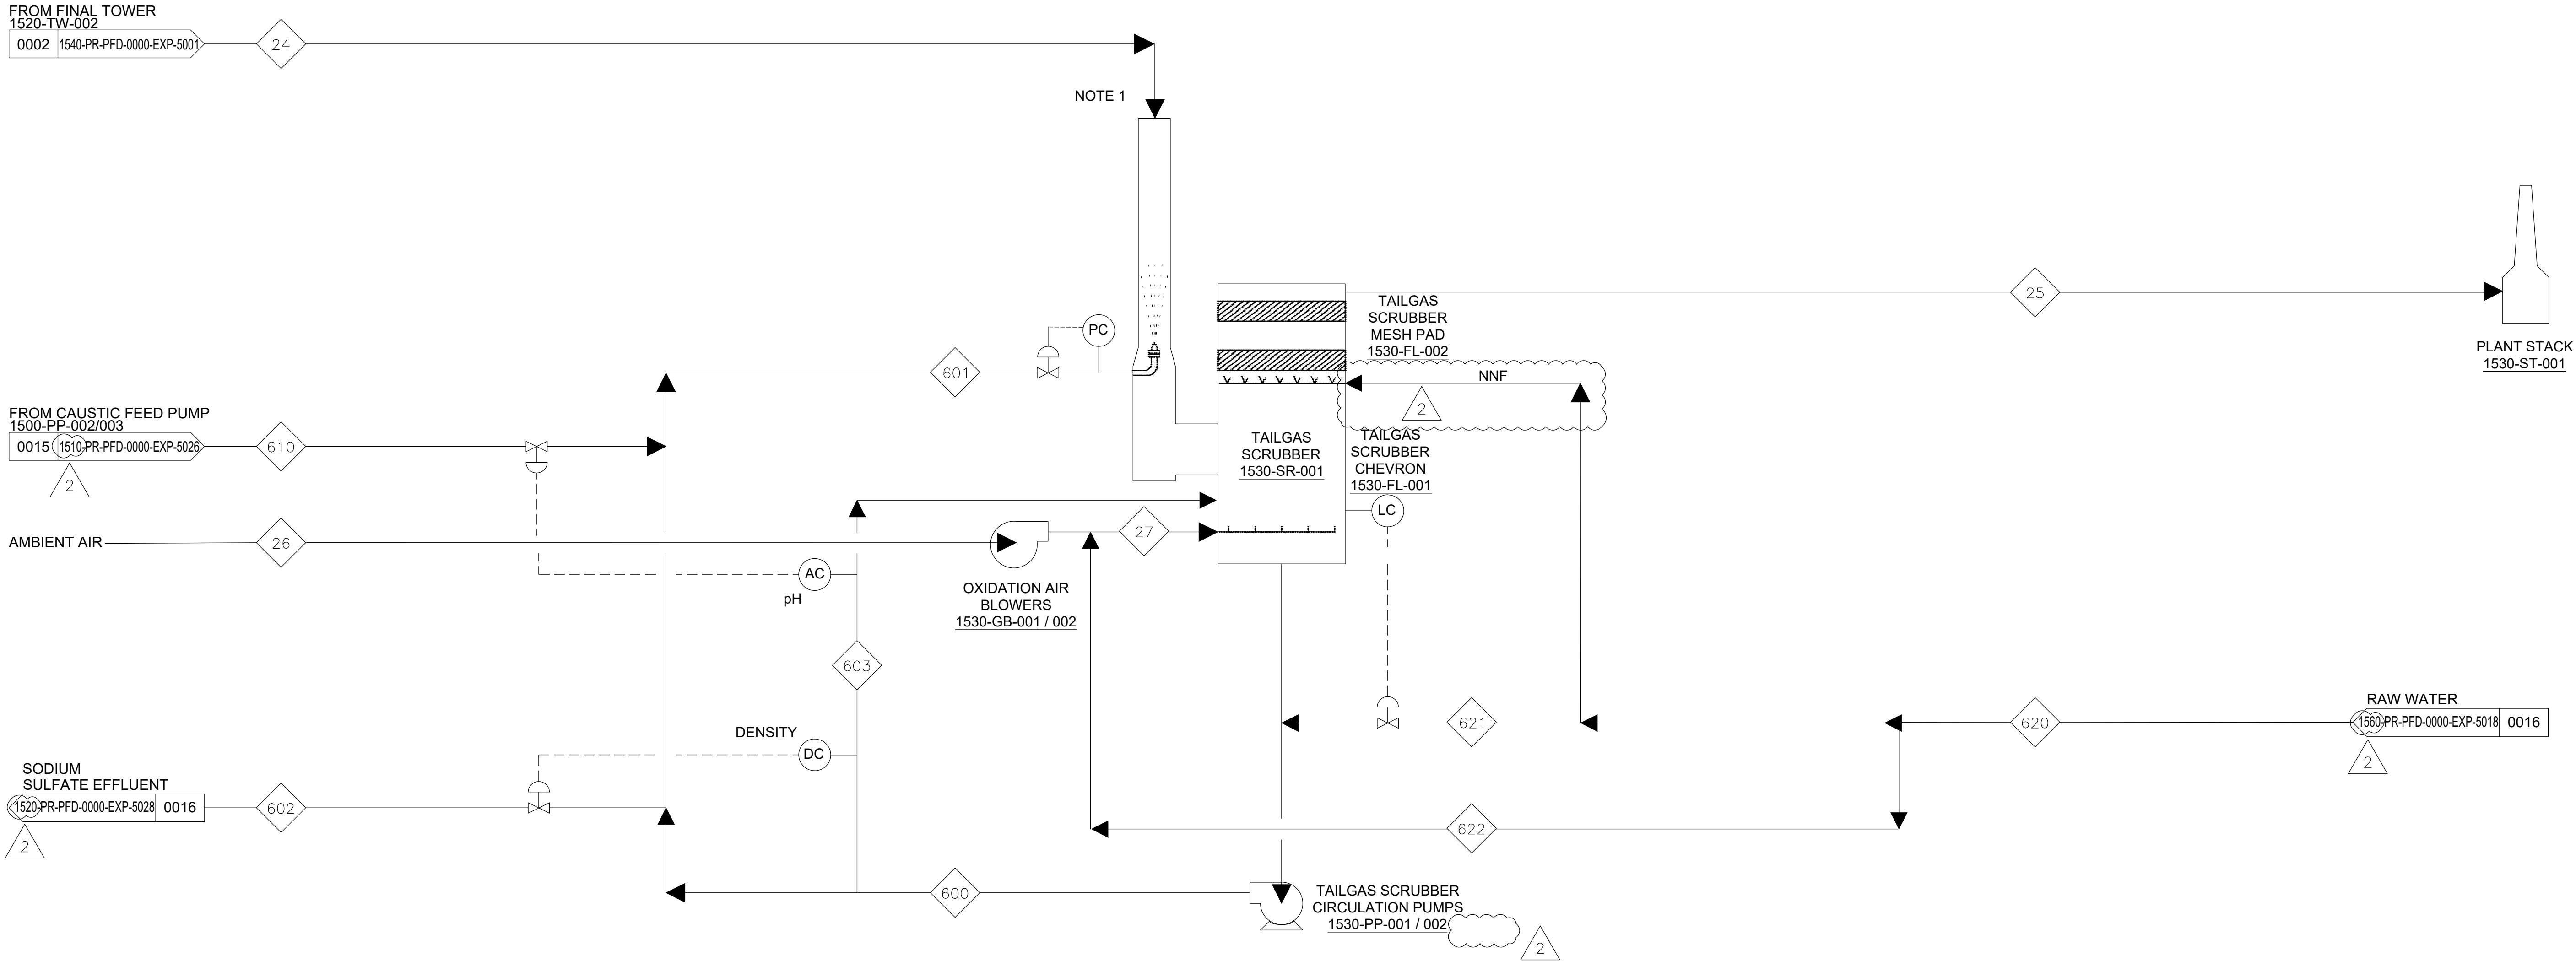

- NOTES:
- INLET BARREL TO HAVE AN ECTFE LINER

NO.	DESCRIPTION	BY	CHK	APP'D	DATE
2	REVISED PUMP QUANTITY				2024-09-23
1	MESH PAD WASH REMOVED	SJ	BA	TV	2024-08-01
0	ISSUED FOR DESIGN	RM	BA	TV	2024-01-16
B	ISSUED FOR CLIENT REVIEW	RM	BA	TV	2023-12-11
A	ISSUED FOR REVIEW	RM	BA		2023-11-23

REVISIONS

SEAL
EXP t +1.713.439.3800 f +1.713.963.9085 exp.com


NOTICE
Property of Lithium Americas Corp (LAC). The contents of this drawing are confidential and proprietary to Lithium Americas Corp. The information contained in this drawing may not be distributed, duplicated, or modified without prior written permission from Lithium Americas Corp. All rights reserved.

SCALE	N/A	SIZE	D
DRAWN BY	R. MASANI	DATE	2024-01-16
CHECKED BY	D. BIRD	DATE	2024-01-16
ENGINEERED BY	B. AFELSKIE	DATE	2024-01-16
APPROVED BY	T. VAN DAELE	DATE	2024-01-16

LithiumAmericas
TITLE
2,250MTPD SA1 - DCDA
PROCESS FLOW DIAGRAM
TAILGAS TREATMENT


THACKER PASS
PROJECT
HUMBOLDT COUNTY, NV

PROJ No. HOU-23001048-A1	REV
DRAWING No. 1530-PR-PFD-0000-EXP-5003	2

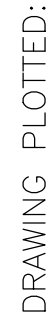

 Elessent MECS® TECHNOLOGIES					PROPRIETARY AND CONFIDENTIAL THE MASTER VERSION OF THIS DOCUMENT IS STORED AS A DIGITAL FILE IN A SOFTWARE ARCHIVE. THIS DOCUMENT IS PRODUCED BY EXP U.S. SERVICES INC. ("EXP") FOR THE LITHIUM NEVADA CORPORATION THACKER PASS SULFURIC ACID PLANT PROJECT ("PROJECT") WHICH IS BASED IN PART ON THE PROCESS DESIGN OF MEC'S, INC. ("MECS"). IT CONTAINS PROPRIETARY AND CONFIDENTIAL INFORMATION AND KNOW-HOW AND MAY INCLUDE PATENTED INTELLECTUAL PROPERTY THAT ARE, IN EACH CASE, PROPERTY OF MEC'S OR EXP (TOGETHER, THE "CONTRACTORS") AND AS SUCH SHALL NOT BE USED, DISCLOSED, DISSEMINATED, PUBLISHED, OR REPRODUCED, IN WHOLE OR IN PART, FOR ANY PURPOSE OTHER THAN FOR WHICH IT WAS SUPPLIED BY EXP, EXCEPT IN ACCORDANCE TO THE TERMS OF THE CONTRACTS ENTERED INTO WITH RESPECT TO THE PROJECT OR WITH WRITTEN PERMISSION OF THE CONTRACTORS."		
NOTICE Property of Lithium Americas Corp (LAC). The contents of this drawing are confidential and proprietary to Lithium Americas Corp. The information contained in this drawing may not be distributed, duplicated, or modified without prior written permission from Lithium Americas Corp. All rights reserved	SCALE	N/A	SIZE	D	LithiumAmericas THACKER PASS PROJECT HUMBOLDT COUNTY, NV	PROJ No. HOU-23001048-A1 REV DRAWING No. 1540-PR-PFD-0000-EXP-5004 2	
	DRAWN BY	R. MASANI	DATE	2024-01-16			
	CHECKED BY	D. BIRD	DATE	2024-01-16			
	ENGINEERED BY	B. APELSKIE	DATE	2024-01-16			
	APPROVED BY	T. VAN DAELE	DATE	2024-01-16			
	TITLE						2,250MTPD SA1 - DCDA PROCESS FLOW DIAGRAM BFW AND STEAM

DRAWING PLOTTED:

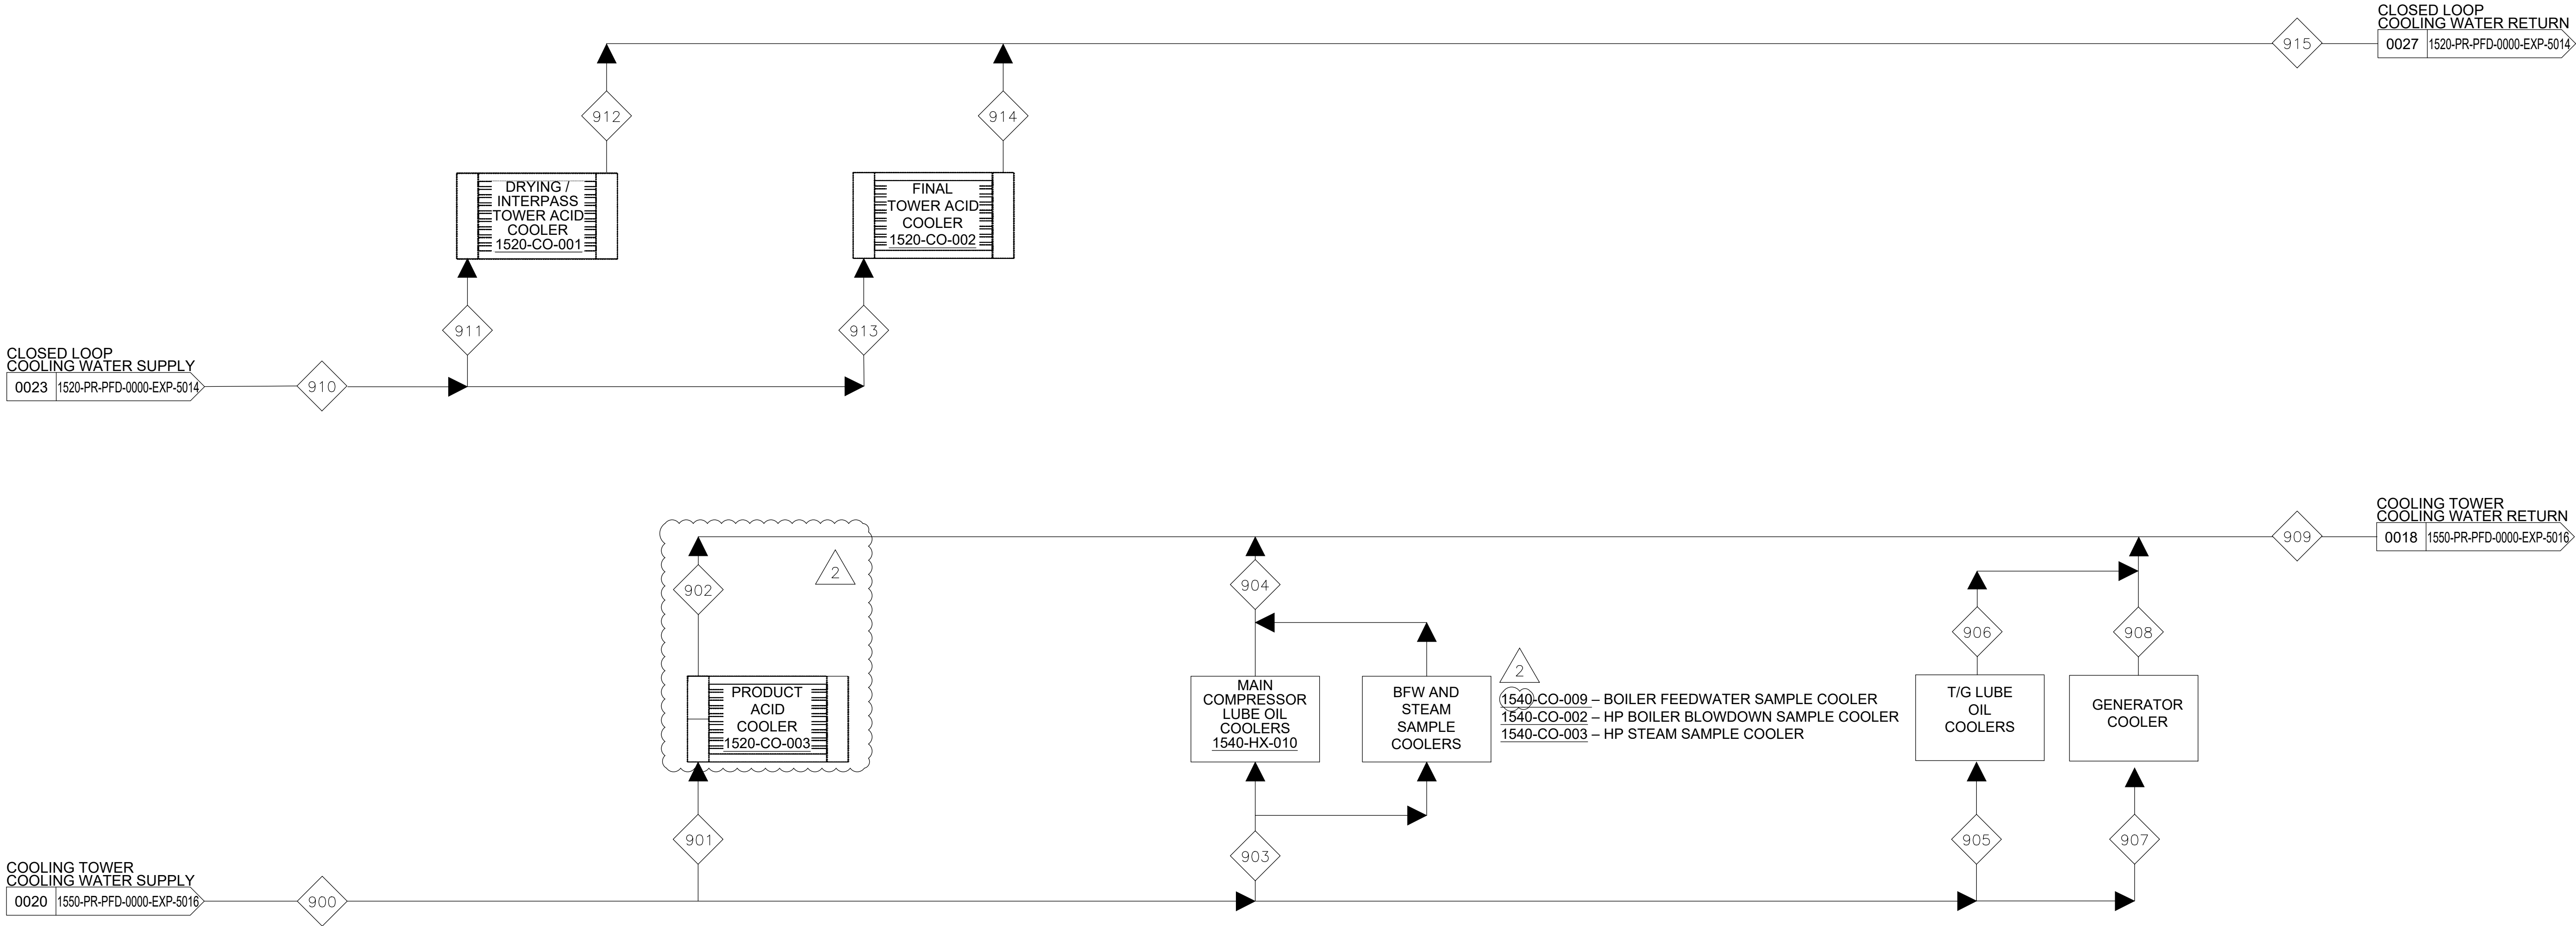

1500-PR-HMB-0000-EXP-5007	MATERIAL BALANCE DESIGN CASE 105 RATE CLEAN
1500-PR-HMB-0000-EXP-5006	MATERIAL BALANCE DESIGN CASE DIRTY
DWG. NO.	TITLE
REFERENCES	

NOTES:	

2	REVISED PRODUCT COOLER REPRESENTATION				2024-09-23
1	RECONFIGURATION FROM HRS READY TO DCDA	SJ	BA	TV	2024-08-01
0	ISSUED FOR DESIGN	RM	BA	TV	2024-01-16
B	ISSUED FOR CLIENT REVIEW	RM	BA	TV	2023-12-11
A	ISSUED FOR REVIEW	RM	BA		2023-11-23
NO.	DESCRIPTION	BY	CHK	APP'D	DATE
REVISIONS					

SEAL
EXP T +1 713 439 3800 F +1 713 963 9085 exp.com

NOTICE
Property of Lithium Americas Corp (LAC). The contents of this drawing are confidential and proprietary to Lithium Americas Corp. The information contained in this drawing may not be distributed, duplicated, or modified without prior written permission from Lithium Americas Corp. All rights reserved.

SCALE
N/A

DRAWN BY
R. MASANI

CHECKED BY
D. BIRD

ENGINEERED BY
B. AFELSKIE

APPROVED BY
T. VAN DAELE

SIZE
D

DATE
2024-01-16

DATE
2024-01-16

DATE
2024-01-16

DATE
2024-01-16

Elessent™
MECS® TECHNOLOGIES

LithiumAmericas

2,250MTPD SA1 - DCDA
PROCESS FLOW DIAGRAM
COOLING WATER

THACKER PASS
PROJECT
HUMBOLDT COUNTY, NV

PROJ No. HOU-23001048-A1


DRAWING No.
1520-PR-PFD-0000-EXP-5005

REV

2

PROPRIETARY AND CONFIDENTIAL
THE MASTER VERSION OF THIS DOCUMENT IS STORED AS A DIGITAL FILE IN A SOFTWARE ARCHIVE. THIS DOCUMENT IS PRODUCED BY EXP U. S. SERVICES INC. ("EXP") FOR THE LITHIUM NEVADA CORPORATION THACKER PASS SULFURIC ACID PLANT PROJECT ("PROJECT") WHICH IS BASED IN PART ON THE PROCESS DESIGN OF MECS, INC. ("MECS"). IT CONTAINS PROPRIETARY AND CONFIDENTIAL INFORMATION AND KNOW-HOW AND MAY INCLUDE PATENTED INTELLECTUAL PROPERTY THAT ARE, IN EACH CASE, PROPERTY OF MECS, OR EXP TOGETHER, THE "CONTRACTORS" AND AS SUCH SHALL NOT BE USED, DISCLOSED, DISSEMINATED, PUBLISHED, OR REPRODUCED, IN WHOLE OR IN PART, FOR ANY PURPOSE OTHER THAN FOR WHICH IT WAS SUPPLIED BY EXP, EXCEPT IN ACCORDANCE TO THE TERMS OF THE CONTRACT(S) ENTERED INTO WITH RESPECT TO THE PROJECT OR WITH WRITTEN PERMISSION OF THE CONTRACTORS."

DRAWING PLOTTED:

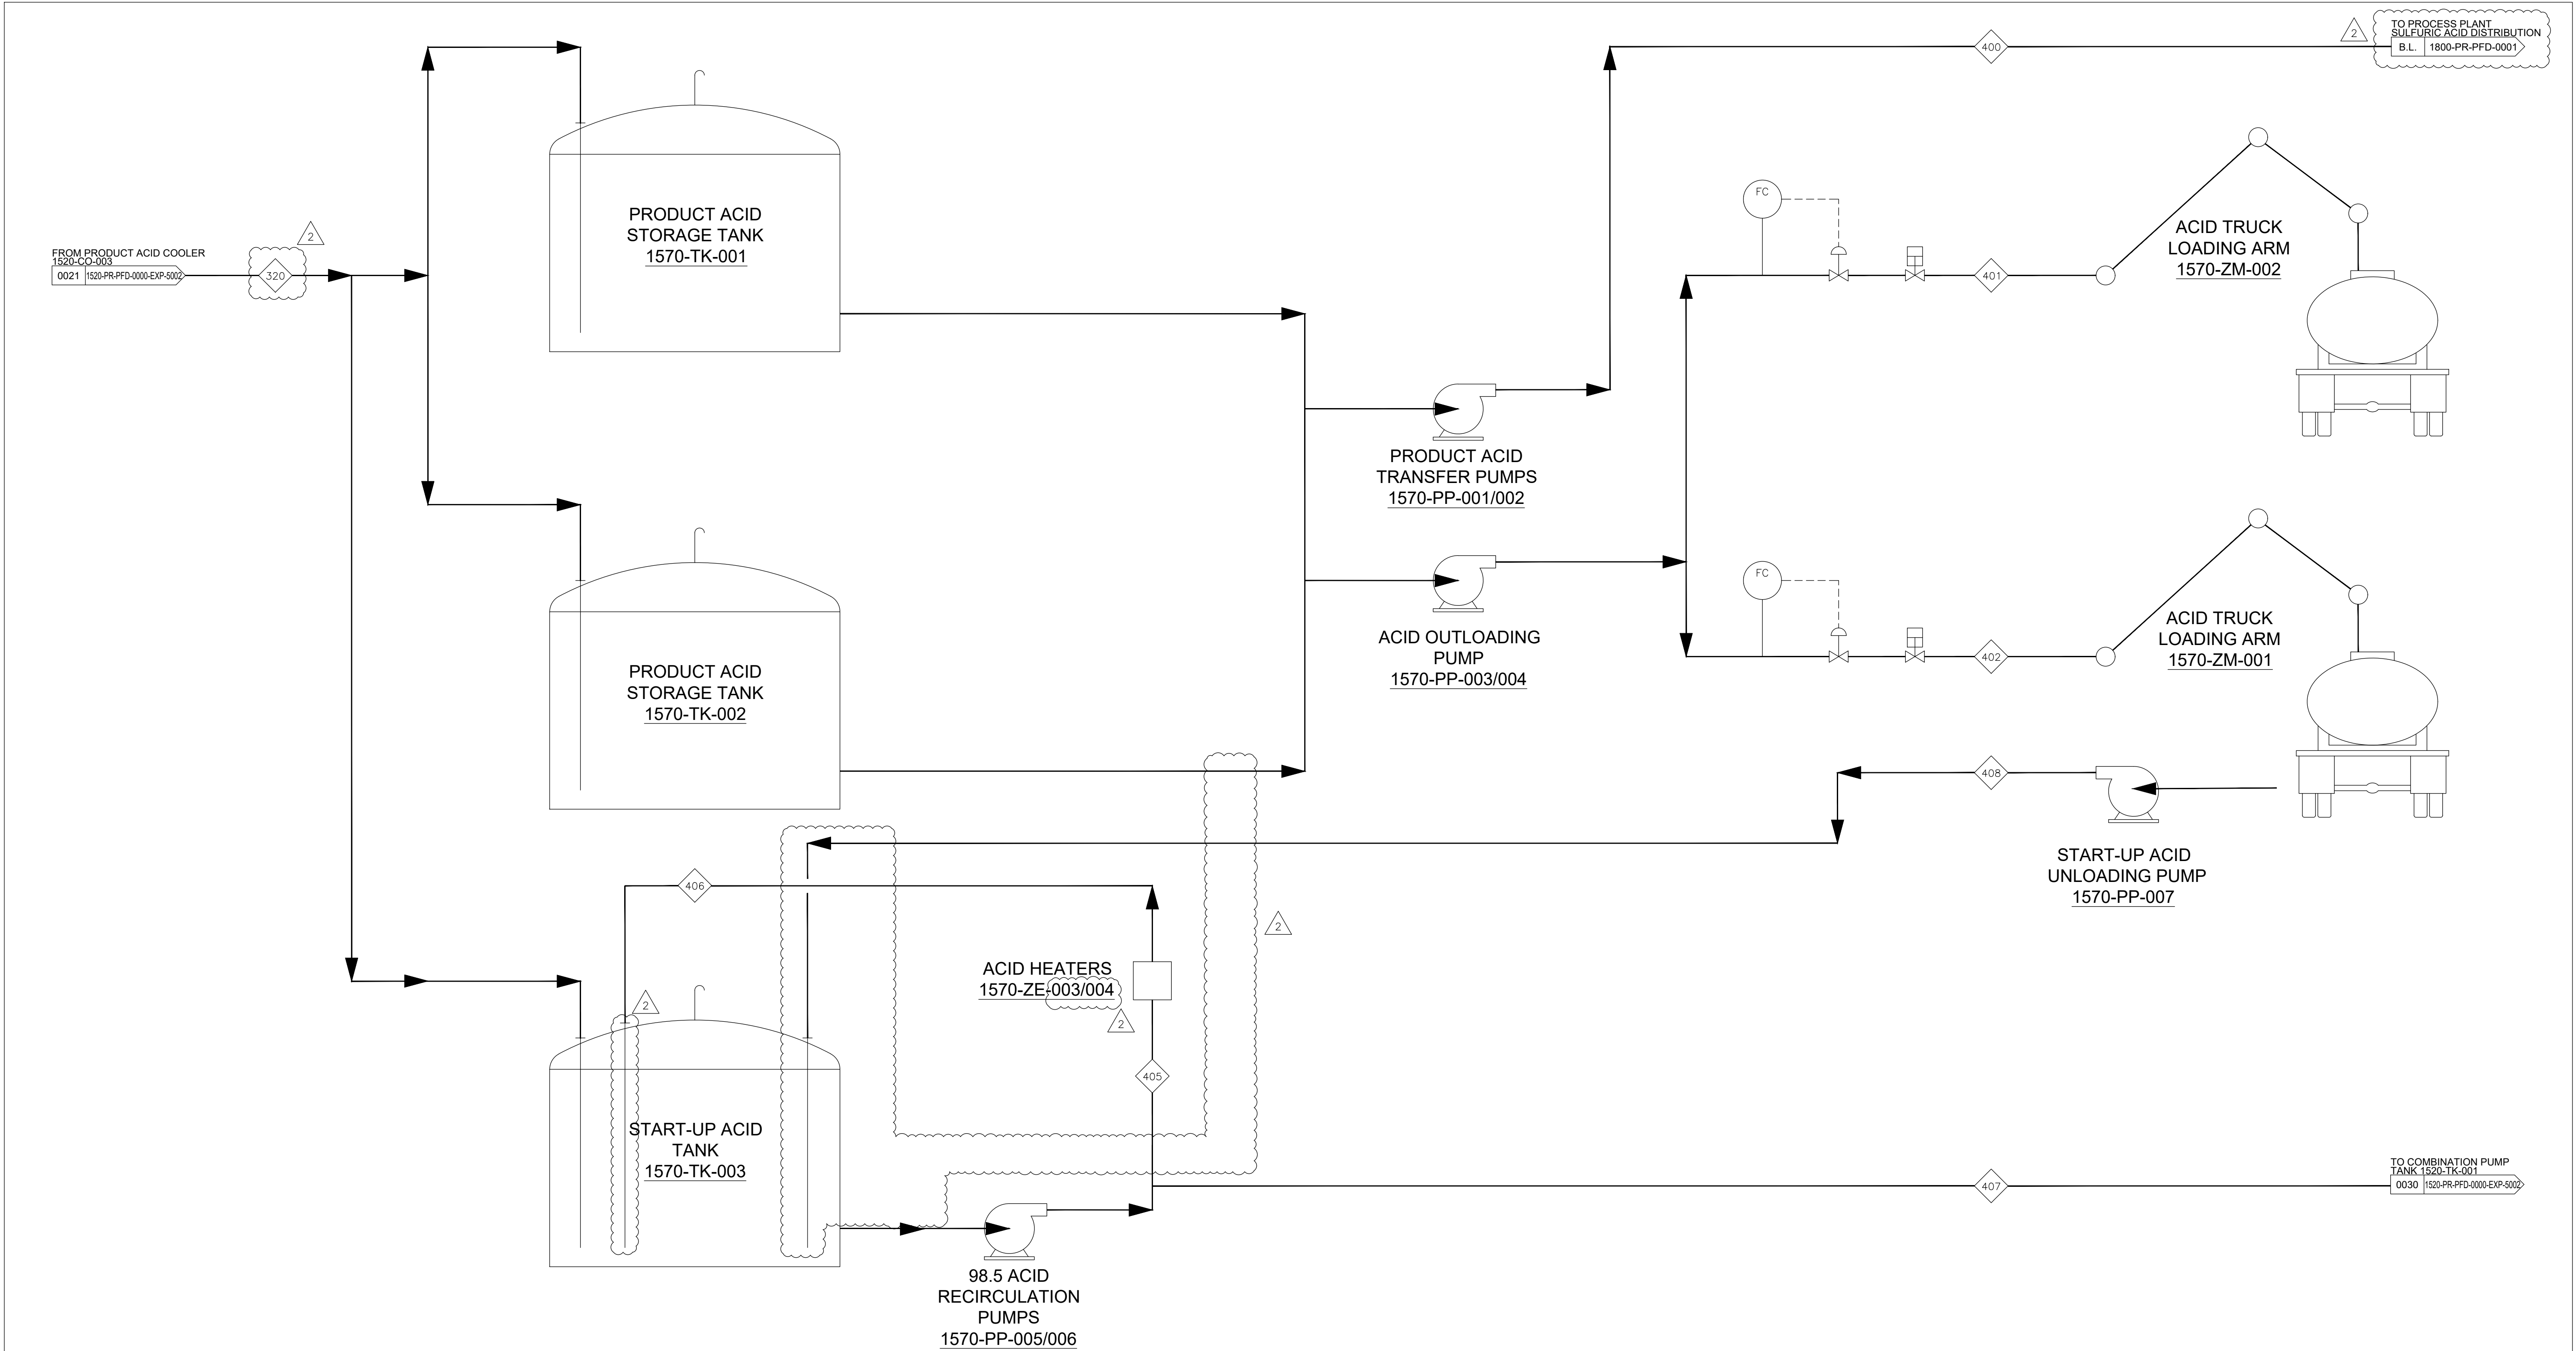


1500-PR-HMB-0000-EXP-5101	MATERIAL BALANCE - DESIGN CASE 105 RATE - UTILITIES
1500-PR-HMB-0000-EXP-5100	MATERIAL BALANCE - DESIGN CASE 100 RATE - UTILITIES
DWG. NO.	TITLE
REFERENCES	

NOTES:	
1. PRODUCT ACID IS 98.5% H2SO4 IN SUMMER AND 93.2% IN WINTER FOR FREEZE PROTECTION.	
2. ACID IN START-UP TANK IS MAINTAINED AT 98.5% YEAR ROUND FOR WINTER START-UPS.	
3. NNF = NORMALLY NO FLOW. LINE 407 IS USED TO MAINTAIN ACID STRENGTH DURING STARTUP.	
PEAK TRANSFER RATE IS 215 GPM.	
4. LINE 408 IS USED FOR INITIAL FILL OF THE START-UP ACID TANK.	

2	DIP PIPES ADDED				2024-09-23
1	PERMANENT START-UP ACID UNLOADING PUMP ADDED	SJ	BA	TV	2024-08-01
0	ISSUED FOR DESIGN	RM	BA	TV	2024-01-16
B	ISSUED FOR CLIENT REVIEW	RM	BA	TV	2023-12-11
A	ISSUED FOR REVIEW	RM	BA		2023-11-23
NO.	DESCRIPTION	BY	CHK	APP'D	DATE
REVISIONS					

SEAL	NOTICE Property of Lithium Americas Corp (LAC). The contents of this drawing are confidential and proprietary to Lithium Americas Corp. The information contained in this drawing may not be distributed, duplicated, or modified without prior written permission from Lithium Americas Corp. All rights reserved	SCALE	SIZE	LithiumAmericas TITLE 2,250MTPD SA1 - DCDA PROCESS FLOW DIAGRAM PRODUCT ACID	THACKER PASS PROJECT HUMBOLDT COUNTY, NV			
		DRAWN BY	DATE					
		R. MASANI	2024-01-16		CHECKED BY	DATE	PROJ No. HOU-23001048-A1	REV
		D. BIRD	2024-01-16		ENGINEERED BY	DATE	DRAWING No.	
		B. AFELSKIE	2024-01-16		APPROVED BY	DATE	1570-PR-PFD-0000-EXP-5010	2
		T. VAN DAELE	2024-01-16					
EXP								
t +1.713.439.3800 f +1.713.963.9085 exp.com								

DRAWING PLOTTED:

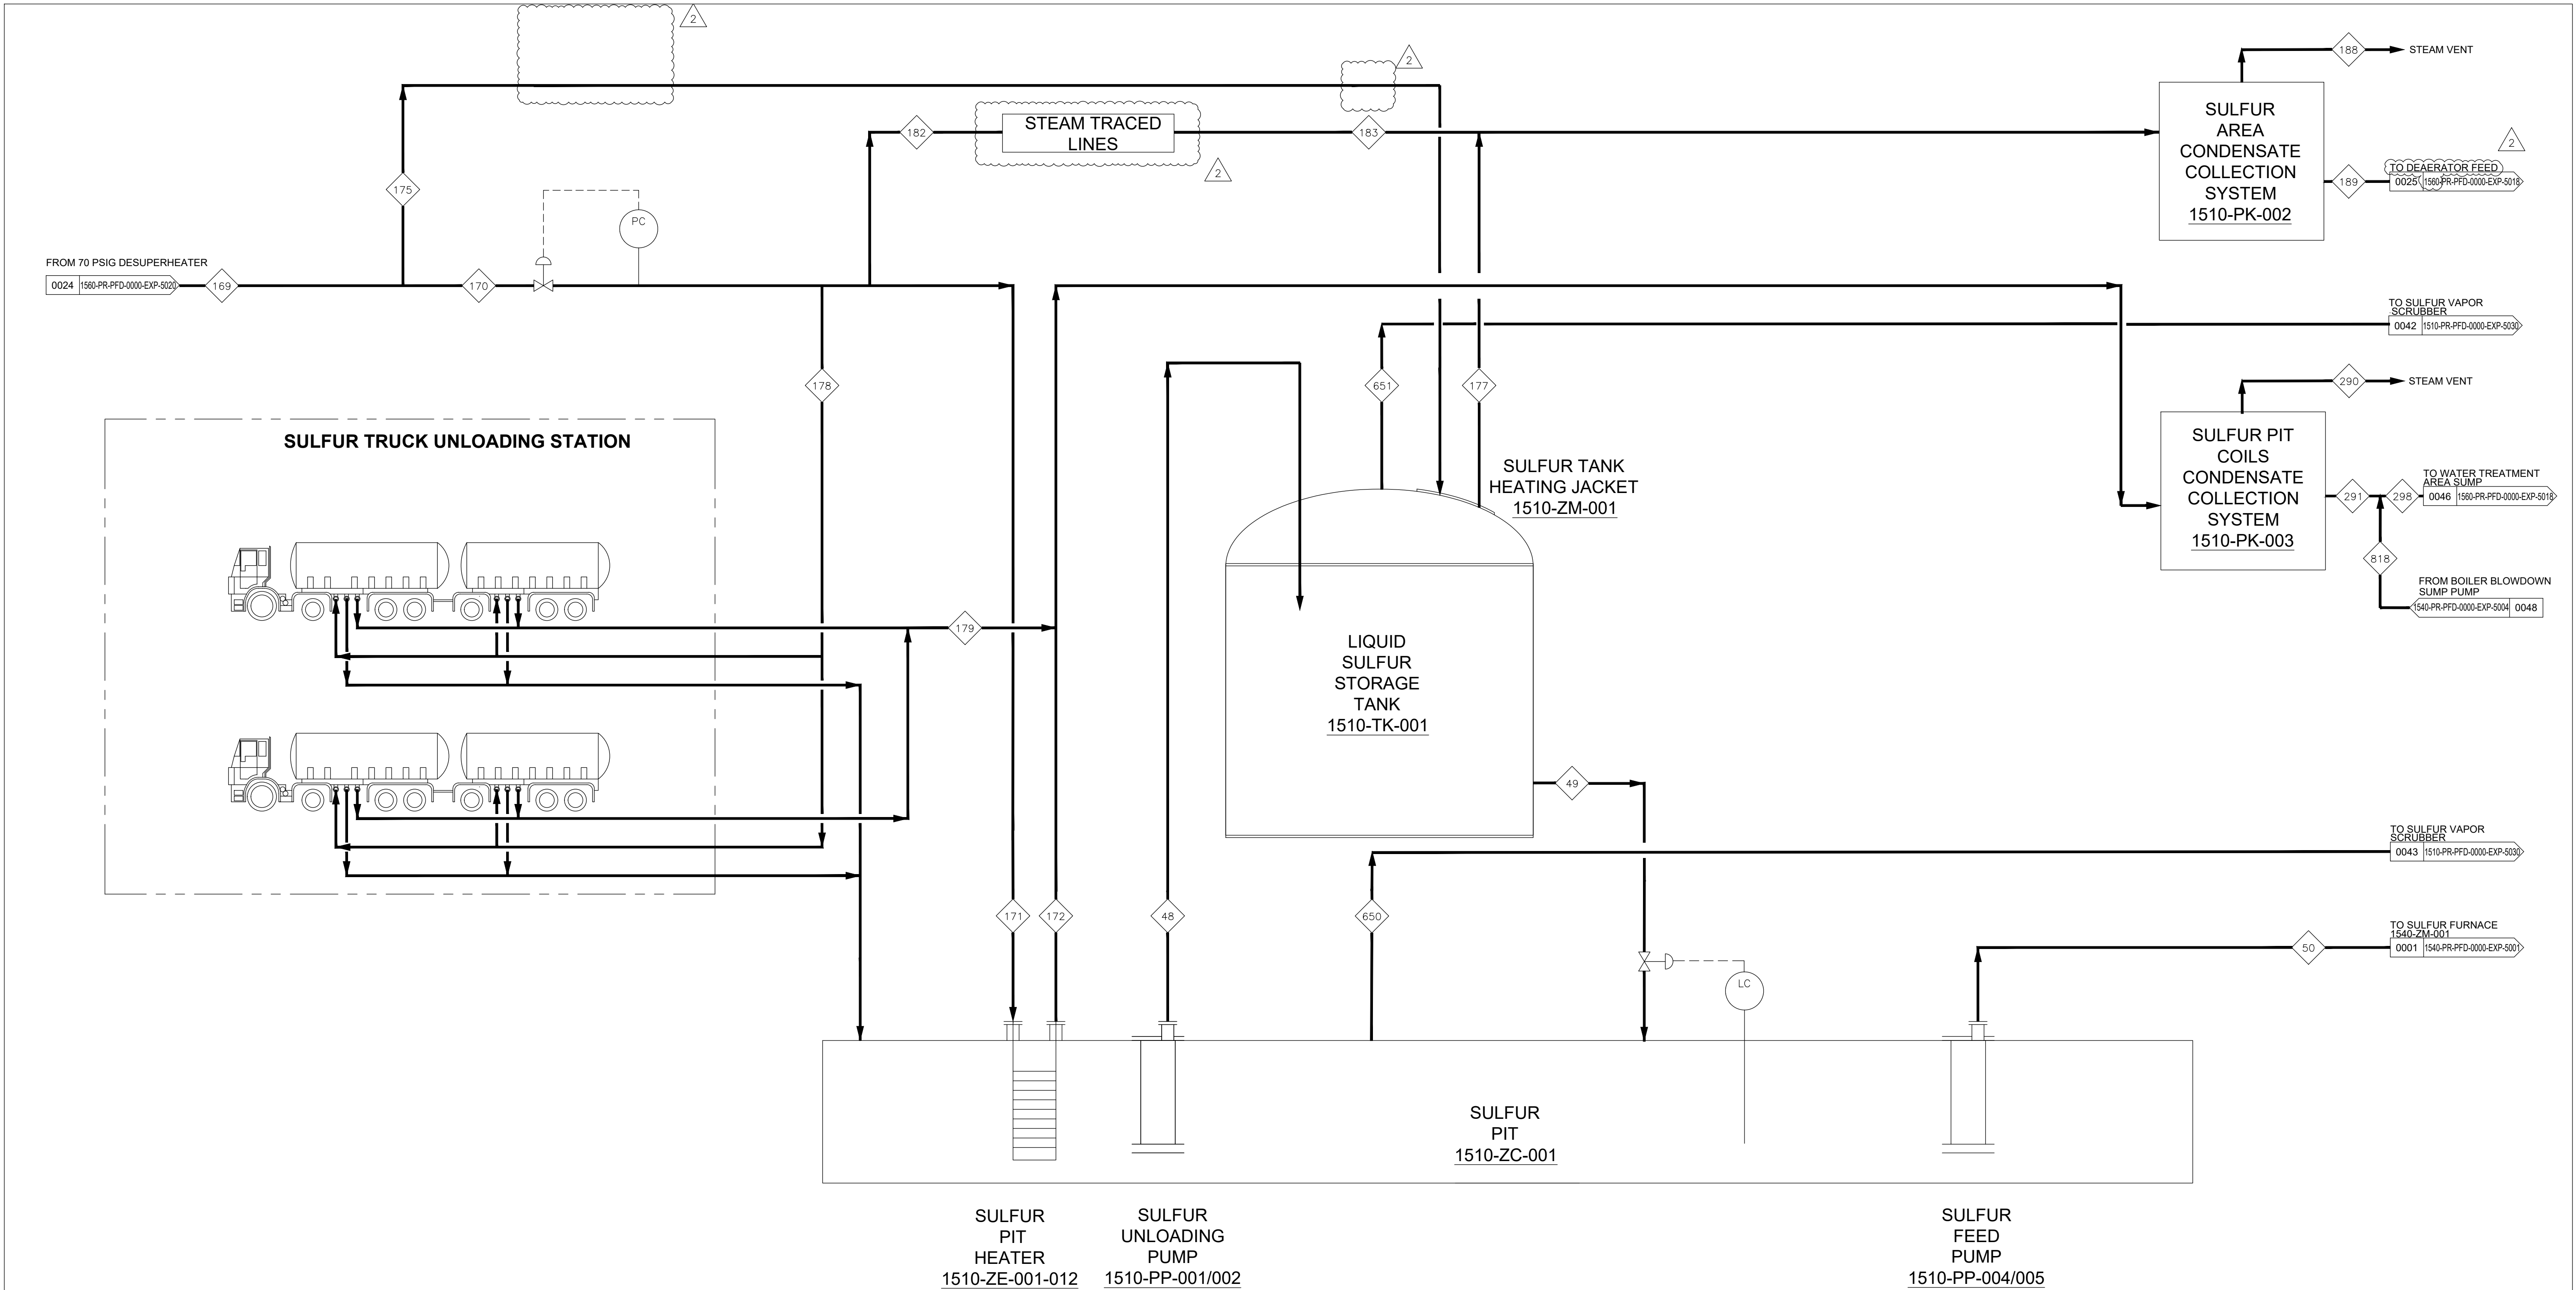

1500-PR-HMB-0000-EXP-5101	MATERIAL BALANCE - DESIGN CASE 105 RATE - UTILITIES
1500-PR-HMB-0000-EXP-5100	MATERIAL BALANCE - DESIGN CASE 100 RATE - UTILITIES
DWG. NO.	TITLE
REFERENCES	

NOTES:	


2	REVISED STEAM PRESSURE TO TANK HEAT TRACING				2024-09-23
1	REVISED SULFUR TANK HEATING METHOD	SJ	BA	TV	2024-08-01
0	ISSUED FOR DESIGN	RM	BA	TV	2024-01-16
B	ISSUED FOR CLIENT REVIEW	RM	BA	TV	2023-12-11
A	ISSUED FOR REVIEW	RM	BA		2023-11-23
NO.	DESCRIPTION	BY	CHK	APP'D	DATE
REVISIONS					

SEAL
EXP T +1 713 439 3600 F +1 713 963 9085 exp.com

NOTICE
Property of Lithium Americas Corp (LAC). The contents of this drawing are confidential and proprietary to Lithium Americas Corp. The information contained in this drawing may not be distributed, duplicated, or modified without prior written permission from Lithium Americas Corp. All rights reserved.


				PROPRIETARY AND CONFIDENTIAL THIS DRAWING IS THE PROPERTY OF EXP. INFORMATION AND KNOW-HOW HEREON ARE CONFIDENTIAL AND PROPRIETARY AND MAY NOT BE USED, REPRODUCED, OR REVEALED TO OTHERS EXCEPT IN ACCORDANCE WITH THE TERMS OF A CONTRACT WITH OR OTHER WRITTEN PERMISSION OF EXP. ANY REPRODUCTIONS IN WHOLE OR PART INCLUDING SHOP DRAWINGS SHALL BEAR OR REFER TO THIS STAMP.	
SCALE N/A	SIZE D			THACKER PASS PROJECT HUMBOLDT COUNTY, NV	
DRAWN BY R. MASANI	DATE 2024-01-16	TITLE 2,250MTPD SA1 - DCDA PROCESS FLOW DIAGRAM SULFUR		PROJ No. HOU-23001048-A1	REV
CHECKED BY D. BIRD	DATE 2024-01-16			DRAWING No. 1510-PR-PFD-0000-EXP-5012	2
ENGINEERED BY B. AFELSKIE	DATE 2024-01-16				
APPROVED BY T. VAN DAELE	DATE 2024-01-16				

DRAWING PLOTTED:

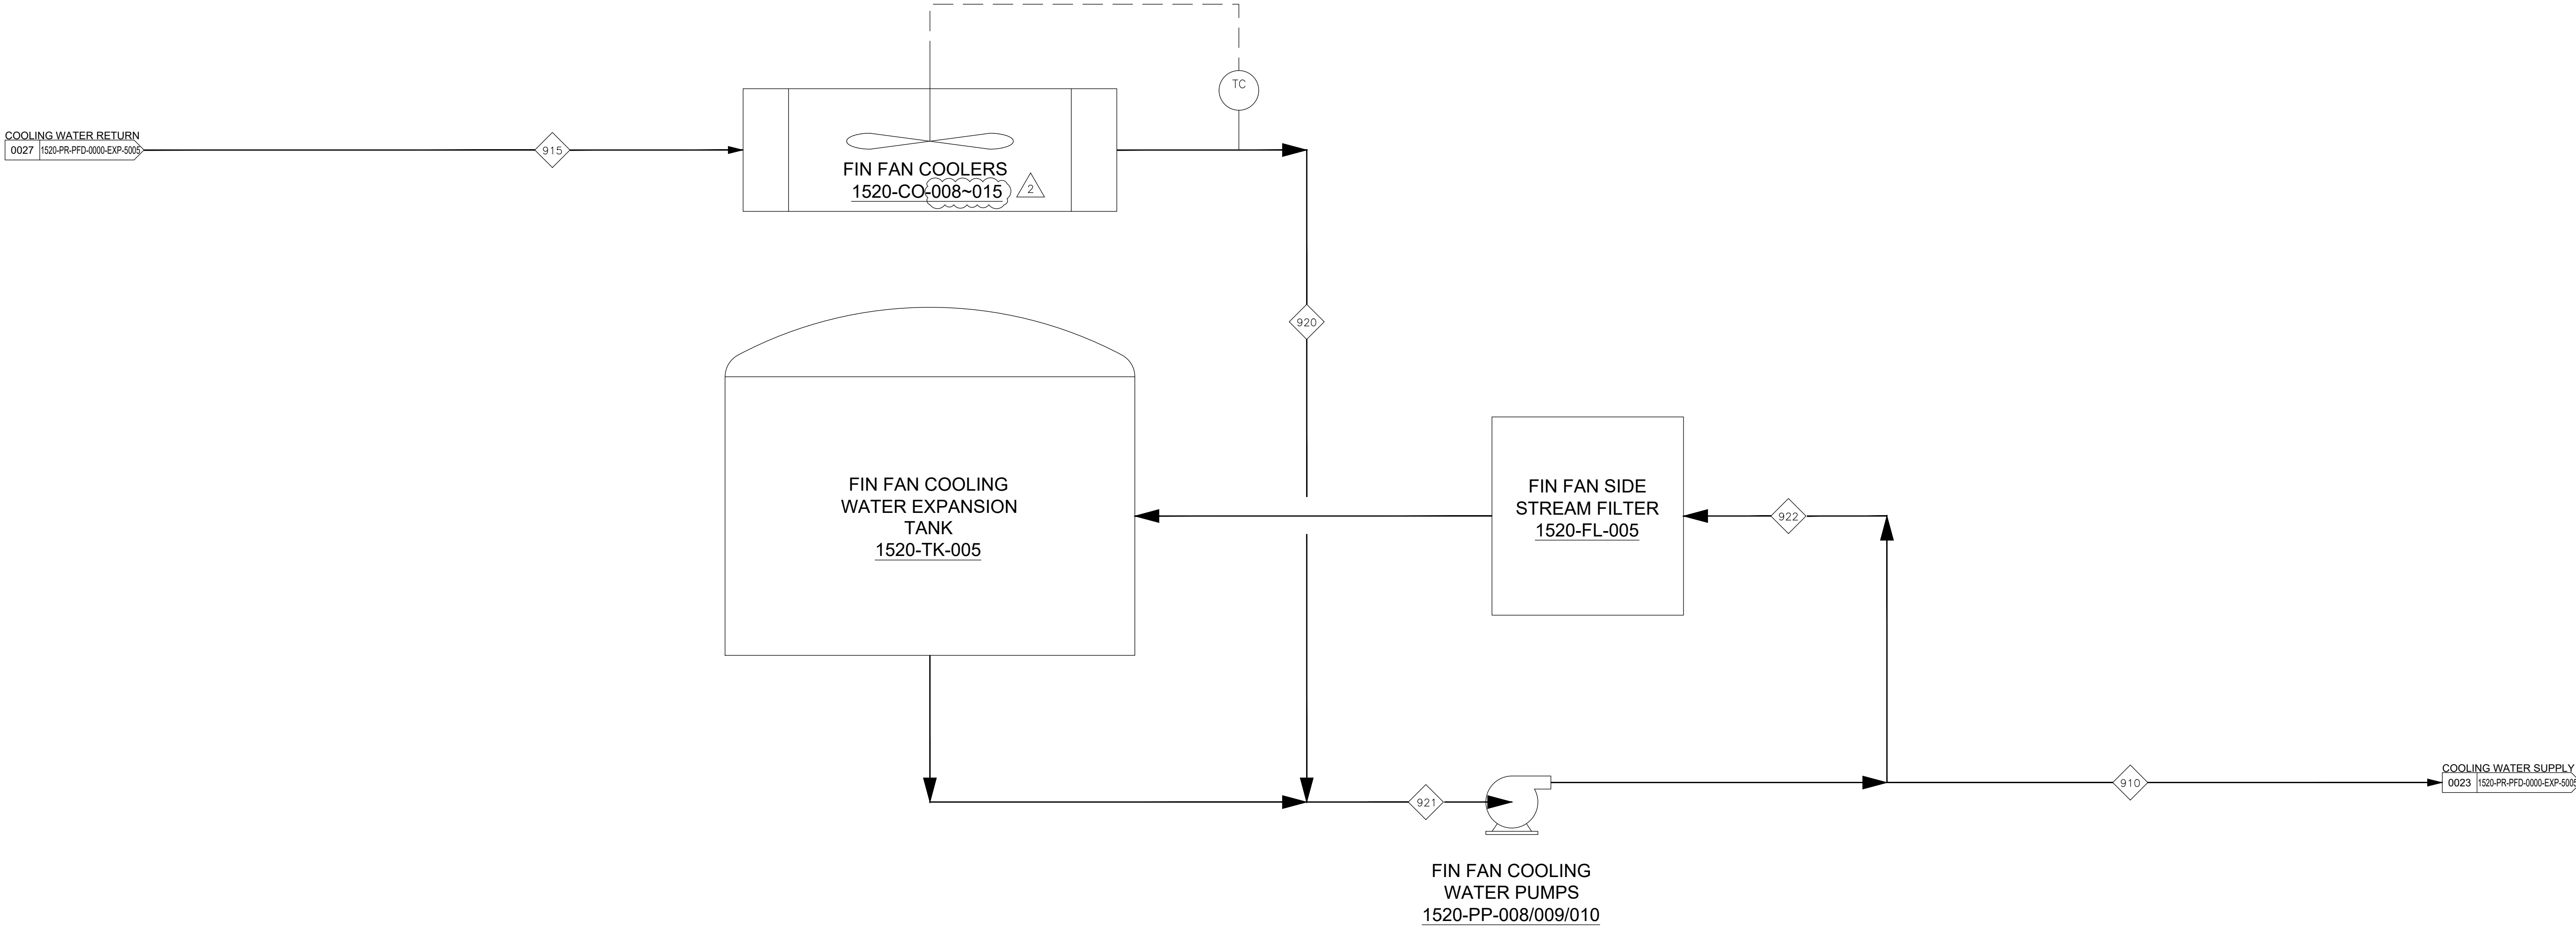

		NOTES:							SEAL	NOTICE Property of Lithium Americas Corp (LAC). The contents of this drawing are confidential and proprietary to Lithium Americas Corp. The information contained in this drawing may not be distributed, duplicated, or modified without prior written permission from Lithium Americas Corp. All rights reserved.	SCALE N/A	SIZE D	 LithiumAmericas	THACKER PASS PROJECT HUMBOLDT COUNTY, NV		
											DRAWN BY R. MASANI	DATE 2024-01-16				TITLE 2,250MTPD SA1 - DCDA PROCESS FLOW DIAGRAM FIN FAN COOLING SYSTEM
											CHECKED BY D. BIRD	DATE 2024-01-16				
											ENGINEERED BY B. AFELSKIE	DATE 2024-01-16		PROJ No. HOU-23001048-A1 DRAWING No. 1520-PR-PFD-0000-EXP-5014	REV 2	
											APPROVED BY T. VAN DAELE	DATE 2024-01-16				
1500-PR-HMB-0000-EXP-5101	MATERIAL BALANCE - DESIGN CASE 105 RATE - UTILITIES		2	REVISED EQUIPMENT TAG				2024-09-23								
			1	REVISED STREAM NUMBER	SJ	BA	TV	2024-08-01								
			0	ISSUED FOR DESIGN	RM	BA	TV	2024-01-16								
			B	ISSUED FOR CLIENT REVIEW	RM	BA	TV	2023-12-08								
1500-PR-HMB-0000-EXP-5100	MATERIAL BALANCE - DESIGN CASE 100 RATE - UTILITIES		A	ISSUED FOR REVIEW	RM	BA		2023-11-23								
DWG. NO.	TITLE		NO.	DESCRIPTION	BY	CHK	APP'D	DATE	EXP T +1.713.439.3600 F +1.713.963.9085 exp.com							
REFERENCES			REVISIONS													


DRAWING PLOTTED:

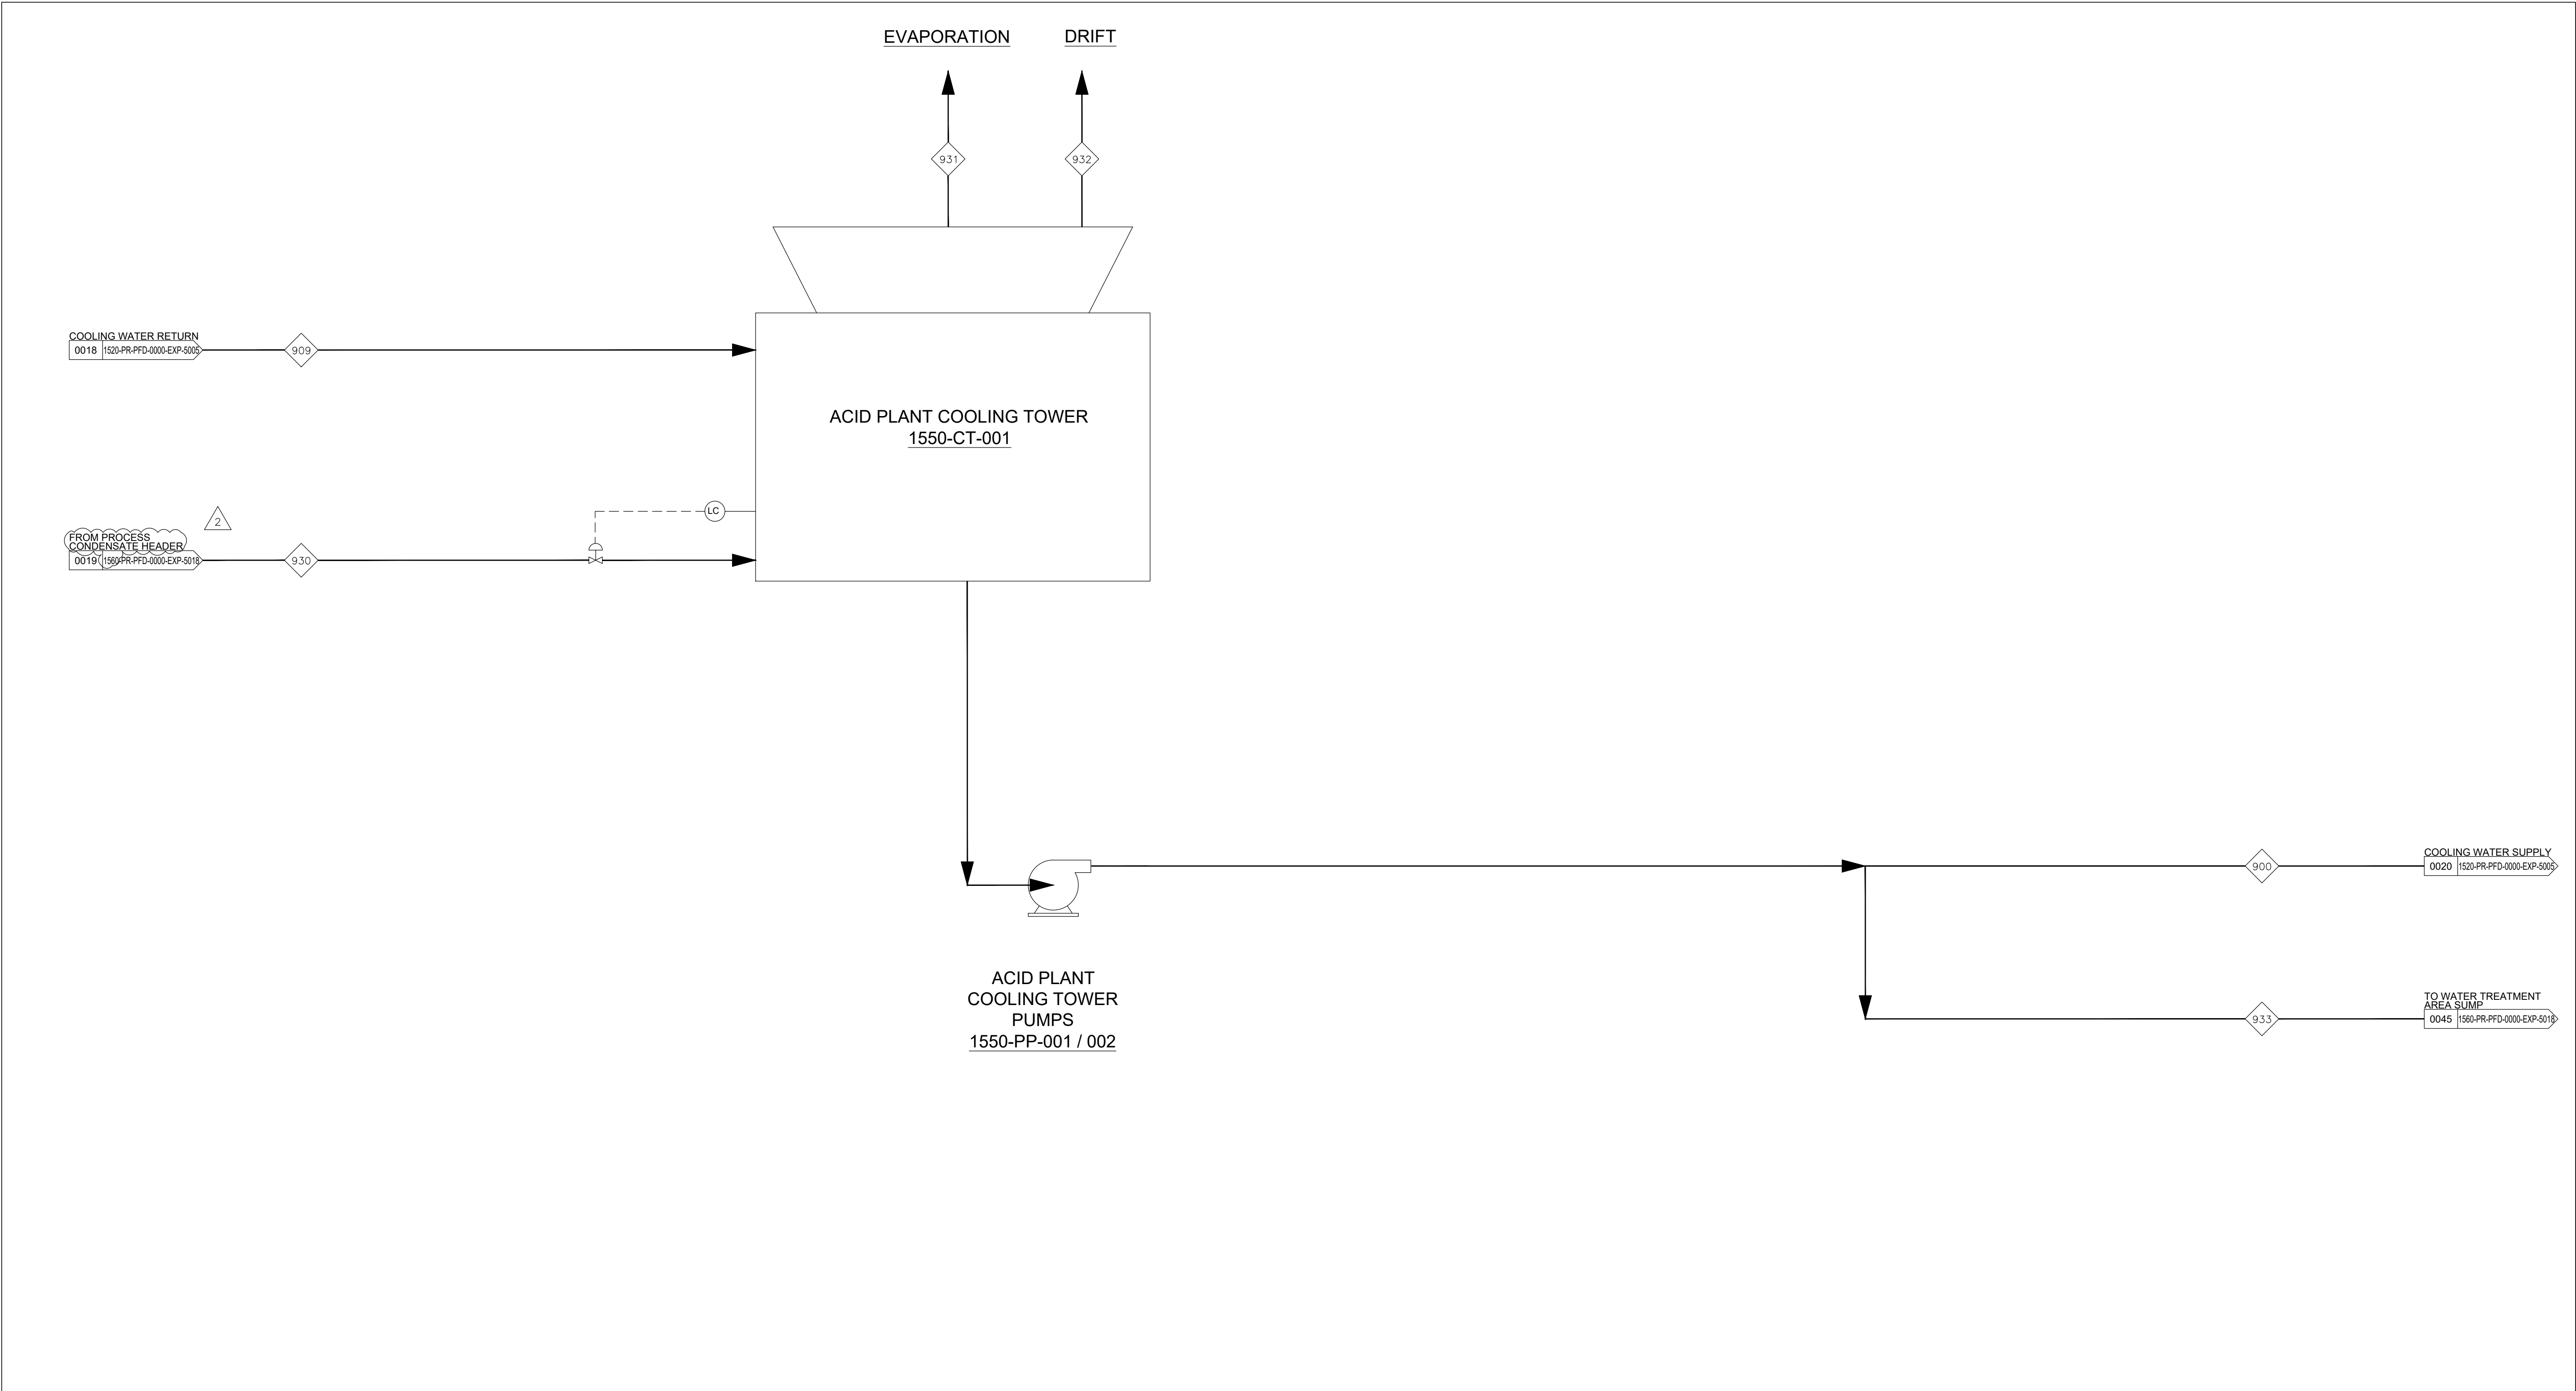

		 PROPRIETARY AND CONFIDENTIAL THIS DRAWING IS THE PROPERTY OF EXP. INFORMATION AND KNOW-HOW HEREON ARE CONFIDENTIAL AND PROPRIETARY AND MAY NOT BE USED, REPRODUCED, OR REVEALED TO OTHERS EXCEPT IN ACCORDANCE WITH THE TERMS OF A CONTRACT WITH OR OTHER WRITTEN PERMISSION OF EXP. ANY REPRODUCTIONS IN WHOLE OR PART INCLUDING SHOP DRAWINGS SHALL BEAR OR REFER TO THIS STAMP.	
		LithiumAmericas 2,250MTPD SA1 - DCDA PROCESS FLOW DIAGRAM ACID PLANT COOLING TOWER THACKER PASS PROJECT HUMBOLDT COUNTY, NV	
		PROJ No. HOU-23001048-A1 DRAWING No. 1550-PR-PFD-0000-EXP-5016	
		REV2	

		NOTES:	</
--	--	--------	--	--	----

DRAWING PLOTTED:

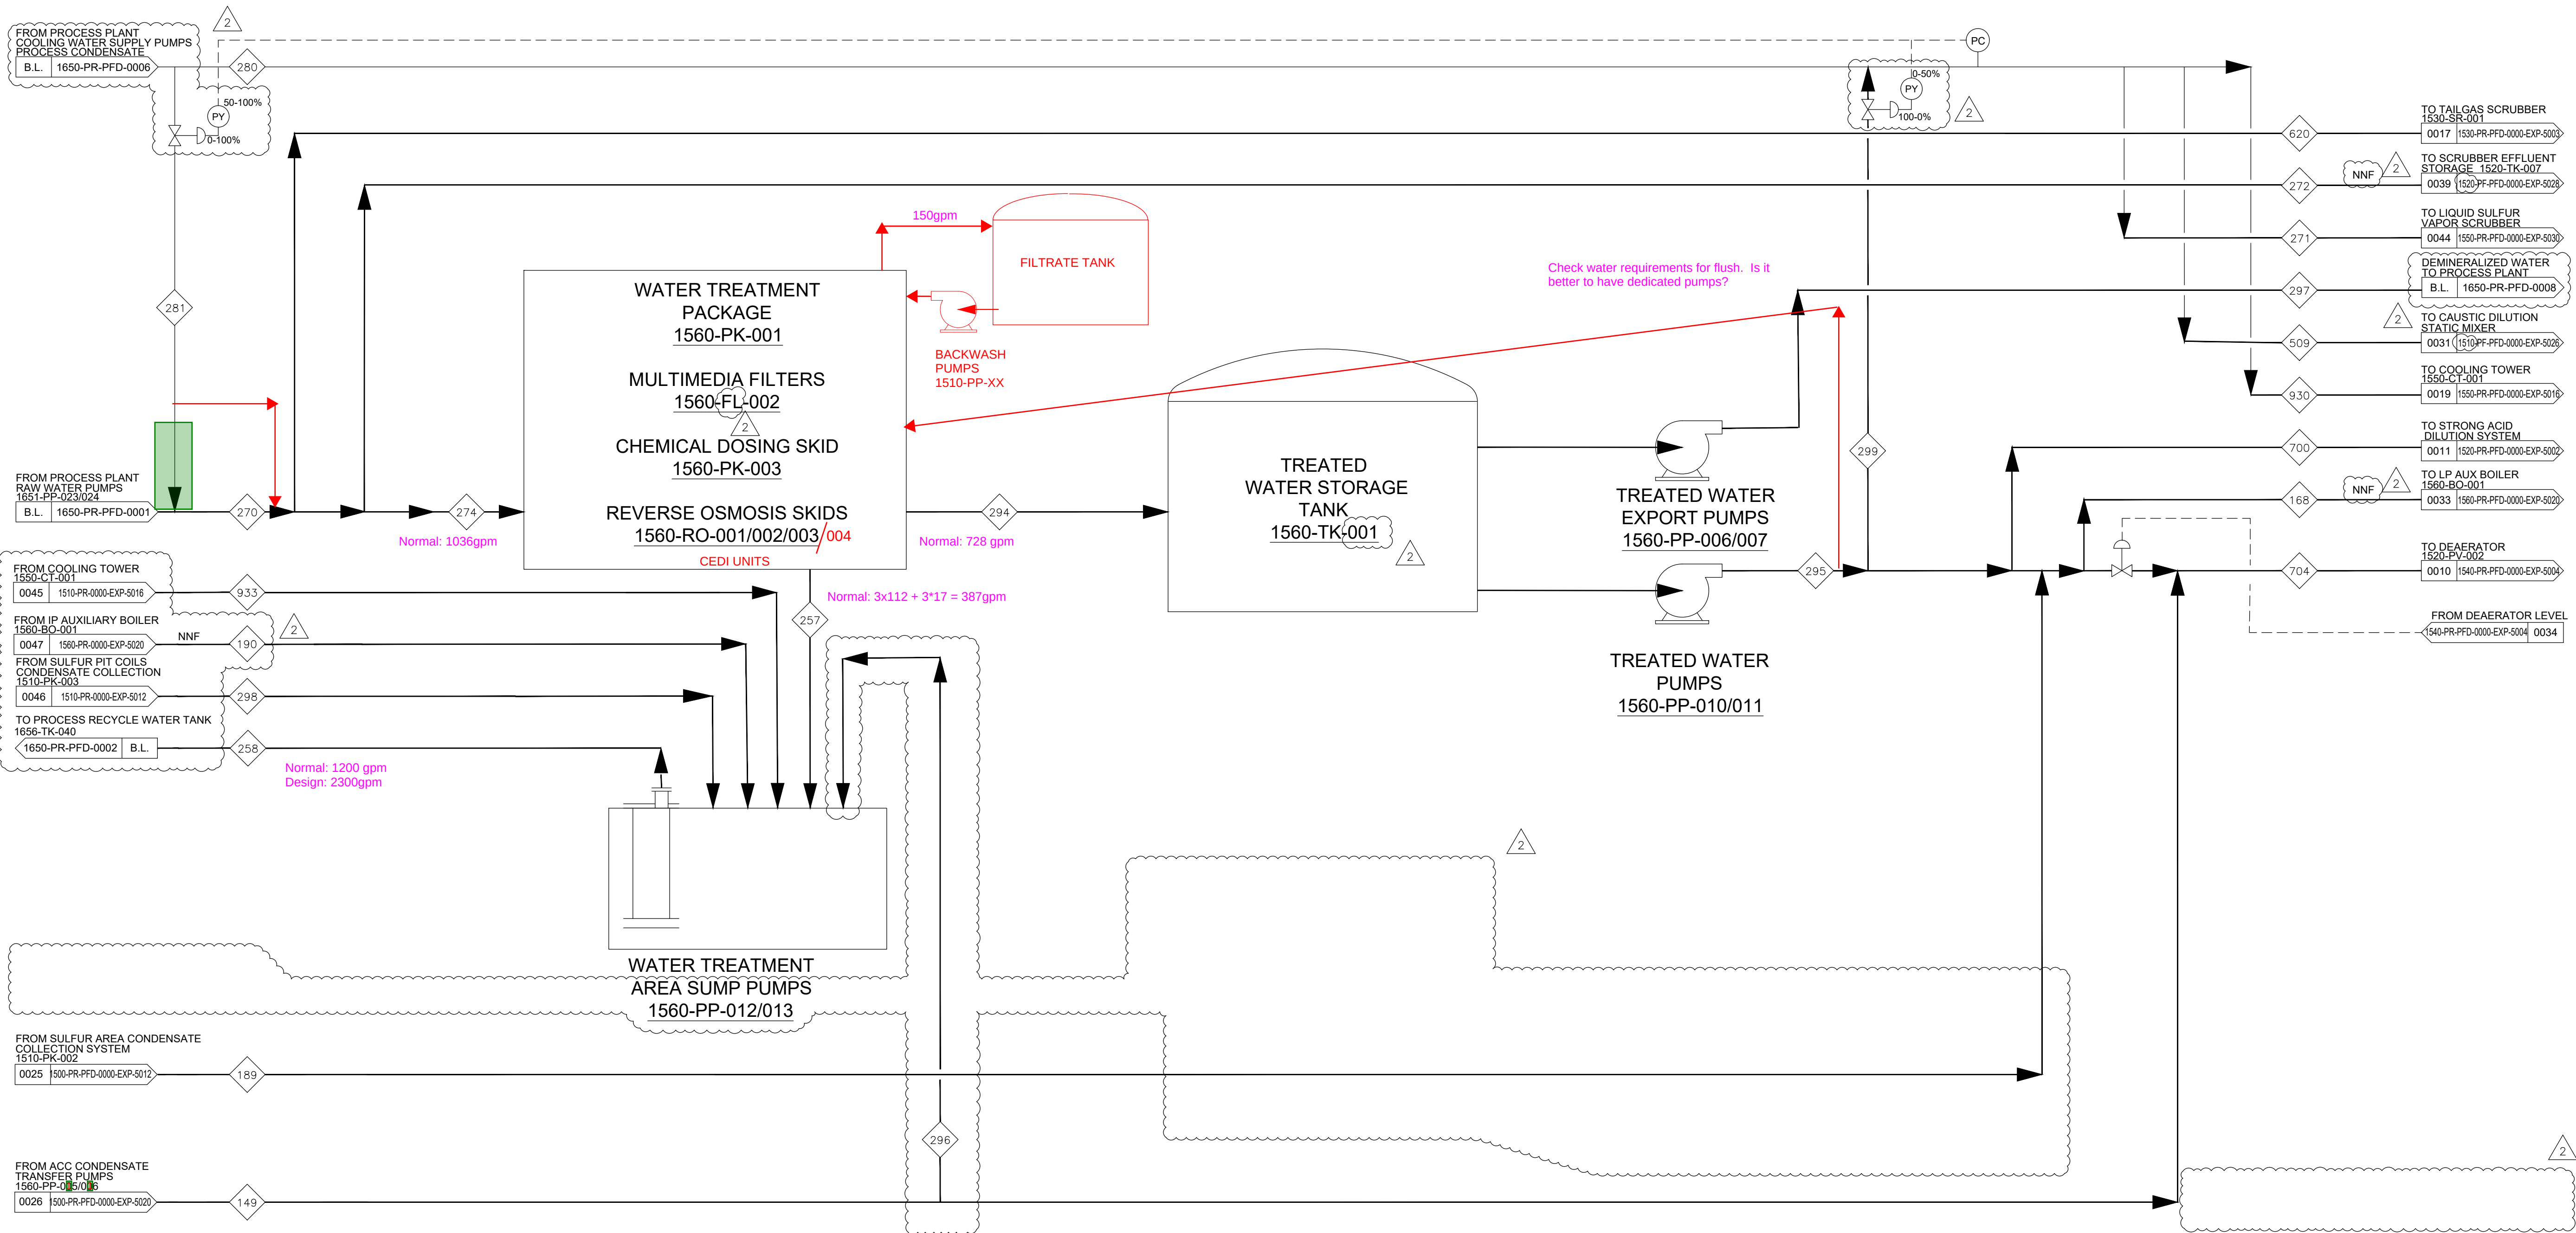

NOTES:

1. NNF=NORMALLY NO FLOW.
2. STREAM 509 IS FLOW REQUIRED TO DURING CAUSTIC TRUCK UNLOADING (1 HOUR DURATION).
3. STREAM 257 AND 294 ARE BASED ON AVERAGE TREATED WATER PRODUCTION RATE.
4. STREAM 258 IS BATCH TRANSFER RATER FROM SUMP.

NO.	DESCRIPTION	BY	CHK	APP'D	DATE
2	STEAM CONDENSATE STORAGE TANK REMOVED				2024-09-23
1	REVISED WATER DISTRIBUTION	SJ	BA	TV	2024-08-01
0	ISSUED FOR DESIGN	RM	BA	TV	2024-01-16
B	ISSUED FOR CLIENT REVIEW	RM	BA	TV	2023-12-11
A	ISSUED FOR REVIEW	RM	BA		2023-11-23


REVISIONS

SEAL


NOTICE
Property of Lithium Americas Corp (LAC). The contents of this drawing are confidential and proprietary to Lithium Americas Corp. The information contained in this drawing may not be distributed, duplicated, or modified without prior written permission from Lithium Americas Corp. All rights reserved.

EXP
T +1.713.439.3600 | F +1.713.963.9085
exp.com

				PROPRIETARY AND CONFIDENTIAL THIS DRAWING IS THE PROPERTY OF EXP. INFORMATION AND KNOW-HOW HEREON ARE CONFIDENTIAL AND PROPRIETARY AND MAY NOT BE USED, REPRODUCED, OR REVEALED TO OTHERS EXCEPT IN ACCORDANCE WITH THE TERMS OF A CONTRACT WITH OR OTHER WRITTEN PERMISSION OF EXP. ANY REPRODUCTIONS IN WHOLE OR PART INCLUDING SHOP DRAWINGS SHALL BEAR OR REFER TO THIS STAMP.	
SCALE	N/A	SIZE	D	LithiumAmericas THACKER PASS PROJECT HUMBOLDT COUNTY, NV	
DRAWN BY	R. MASANI	DATE	2024-01-16		
CHECKED BY	D. BIRD	DATE	2024-01-16		
ENGINEERED BY	B. AFELSKJE	DATE	2024-01-16		
APPROVED BY	T. VAN DAELE	DATE	2024-01-16		
2,250MTPD SA1 - DCDA PROCESS FLOW DIAGRAM WATER TREATMENT				PROJ No. HOU-23001048-A1 DRAWING No. 1560-PR-PFD-0000-EXP-5018	REV 2

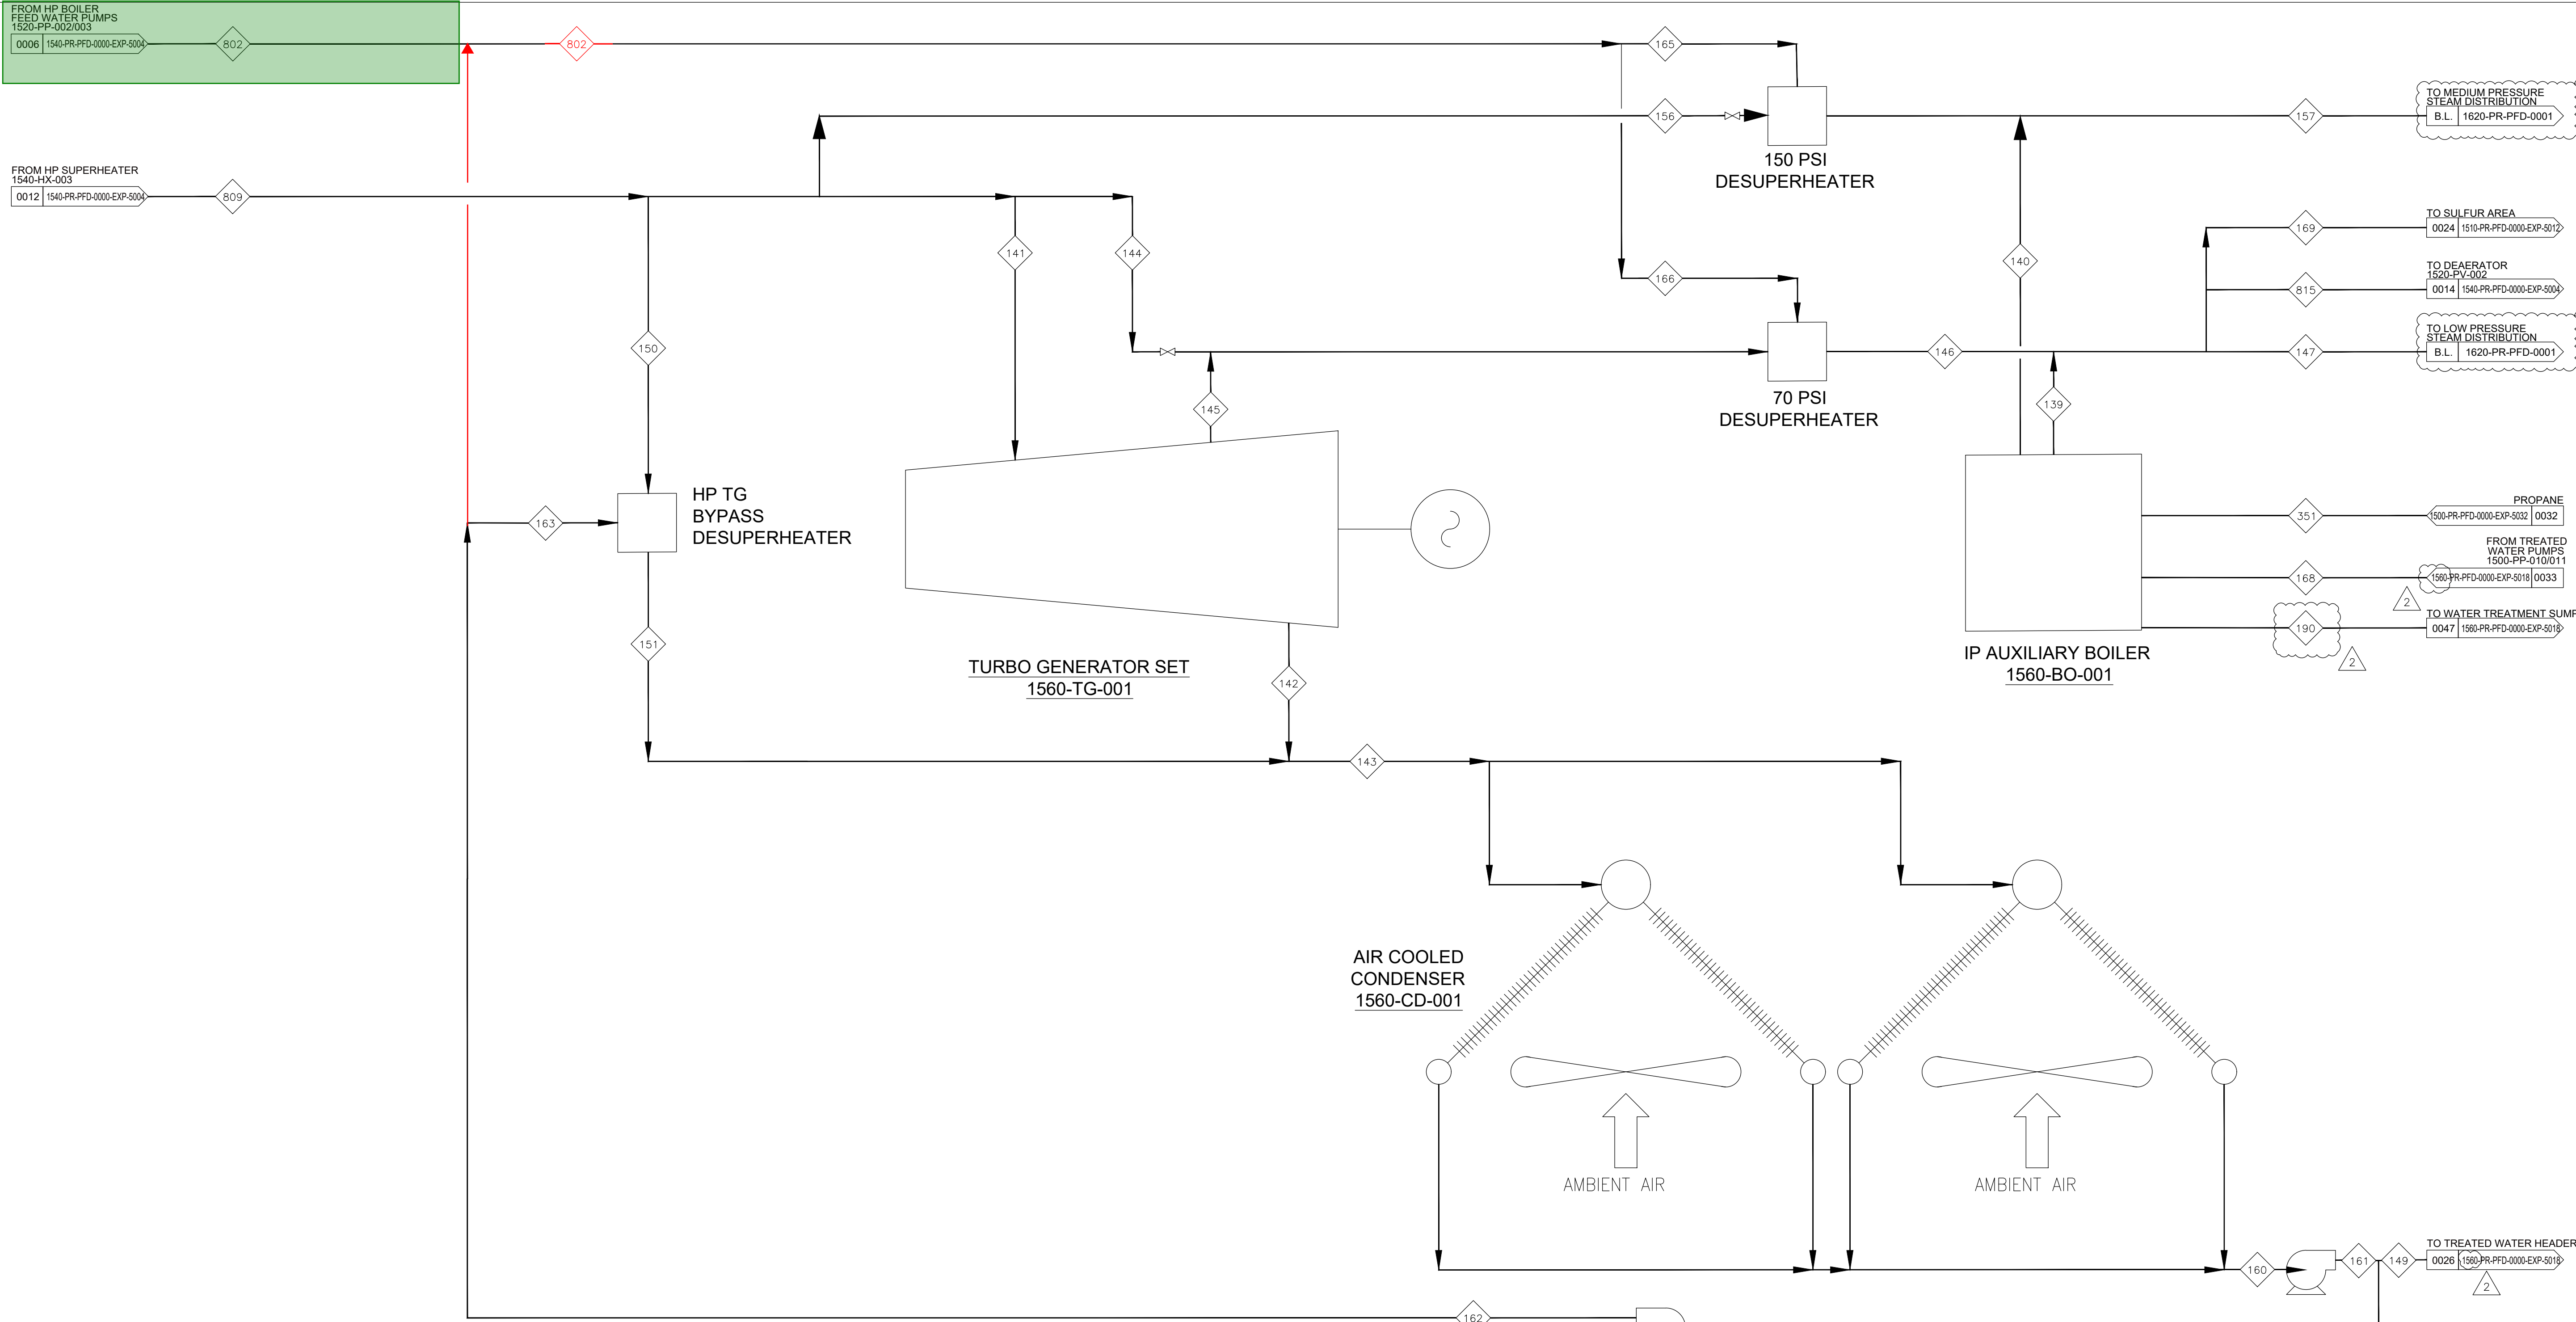[illegible]

DRAWING PLOTTED:

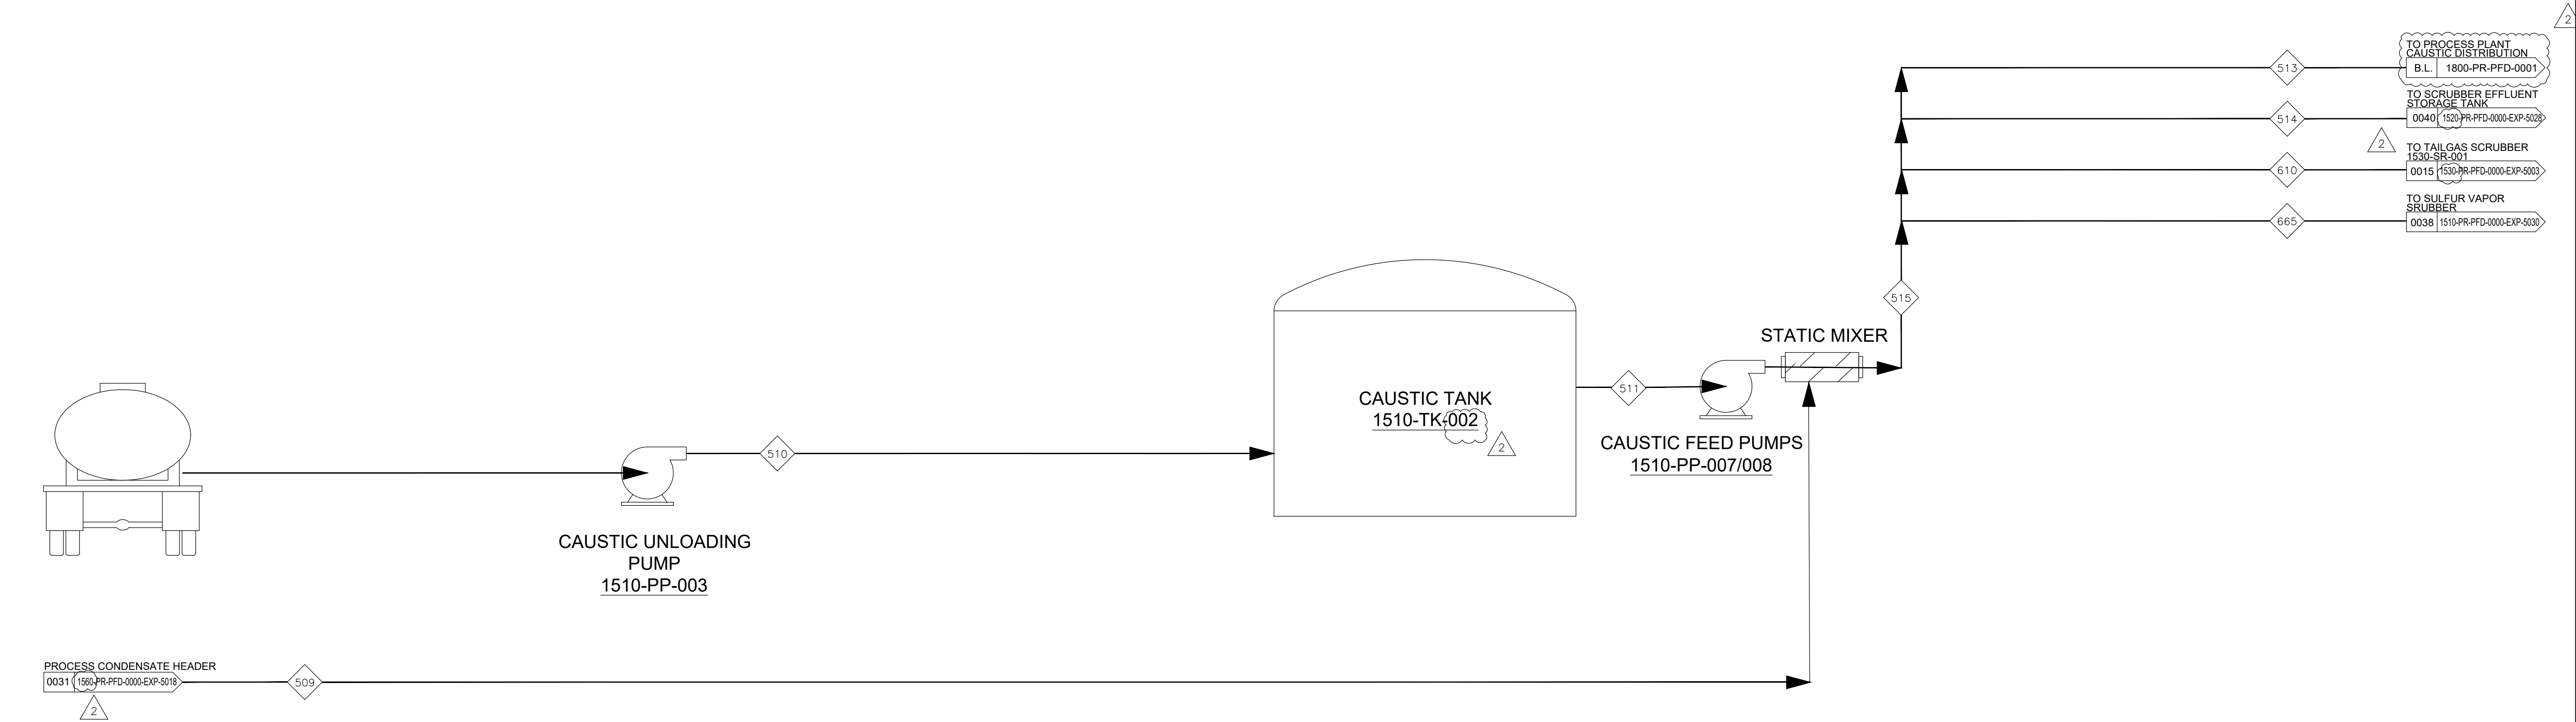

1500-PR-HMB-0000-EXP-5101	MATERIAL BALANCE - DESIGN CASE 105 RATE - UTILITIES
1500-PR-HMB-0000-EXP-5100	MATERIAL BALANCE - DESIGN CASE 100 RATE - UTILITIES
DWG. NO.	TITLE
REFERENCES	

NOTES:	
1. FLOWRATES BASED ON 1 HOUR UNLOAD TIME.	


2	REVISED EQUIPMENT TANK AND OPC DESTINATION				2024-09-23
1	REVISED CAUSTIC STORAGE CONCENTRATION	SJ	BA	TV	2024-08-01
0	ISSUED FOR DESIGN	RM	BA	TV	2024-01-16
B	ISSUED FOR CLIENT REVIEW	RM	BA	TV	2023-12-11
A	ISSUED FOR REVIEW	RM	BA		2023-11-23
NO.	DESCRIPTION	BY	CHK	APP'D	DATE
REVISIONS					

SEAL
EXP
+1.713.439.3800 +1.713.963.9085
exp.com

NOTICE
Property of Lithium Americas Corp (LAC). The contents of this drawing are confidential and proprietary to Lithium Americas Corp. The information contained in this drawing may not be distributed, duplicated, or modified without prior written permission from Lithium Americas Corp. All rights reserved.

SCALE		SIZE		exp.		PROPRIETARY AND CONFIDENTIAL THIS DRAWING IS THE PROPERTY OF EXP. INFORMATION AND KNOW-HOW HEREON ARE CONFIDENTIAL AND PROPRIETARY AND MAY NOT BE USED, REPRODUCED, OR REVEALED TO OTHERS EXCEPT IN ACCORDANCE WITH THE TERMS OF A CONTRACT WITH OR OTHER WRITTEN PERMISSION OF EXP. ANY REPRODUCTIONS IN WHOLE OR PART INCLUDING SHOP DRAWINGS SHALL BEAR OR REFER TO THIS STAMP.	
N/A		D		LithiumAmericas		THACKER PASS PROJECT HUMBOLDT COUNTY, NV	
DRAWN BY	R. MASANI	DATE	2024-01-16	TITLE		PROJ No.	HOU-23001048-A1
CHECKED BY	D. BIRD	DATE	2024-01-16	2,250MTPD SA1 - DCDA PROCESS FLOW DIAGRAM 20% CAUSTIC SODA SUPPLY		REV	
ENGINEERED BY	B. AFELSKIE	DATE	2024-01-16			1510-PR-PFD-0000-EXP-5026	2
APPROVED BY	T. VAN DAELE	DATE	2024-01-16				

DRAWING PLOTTED:

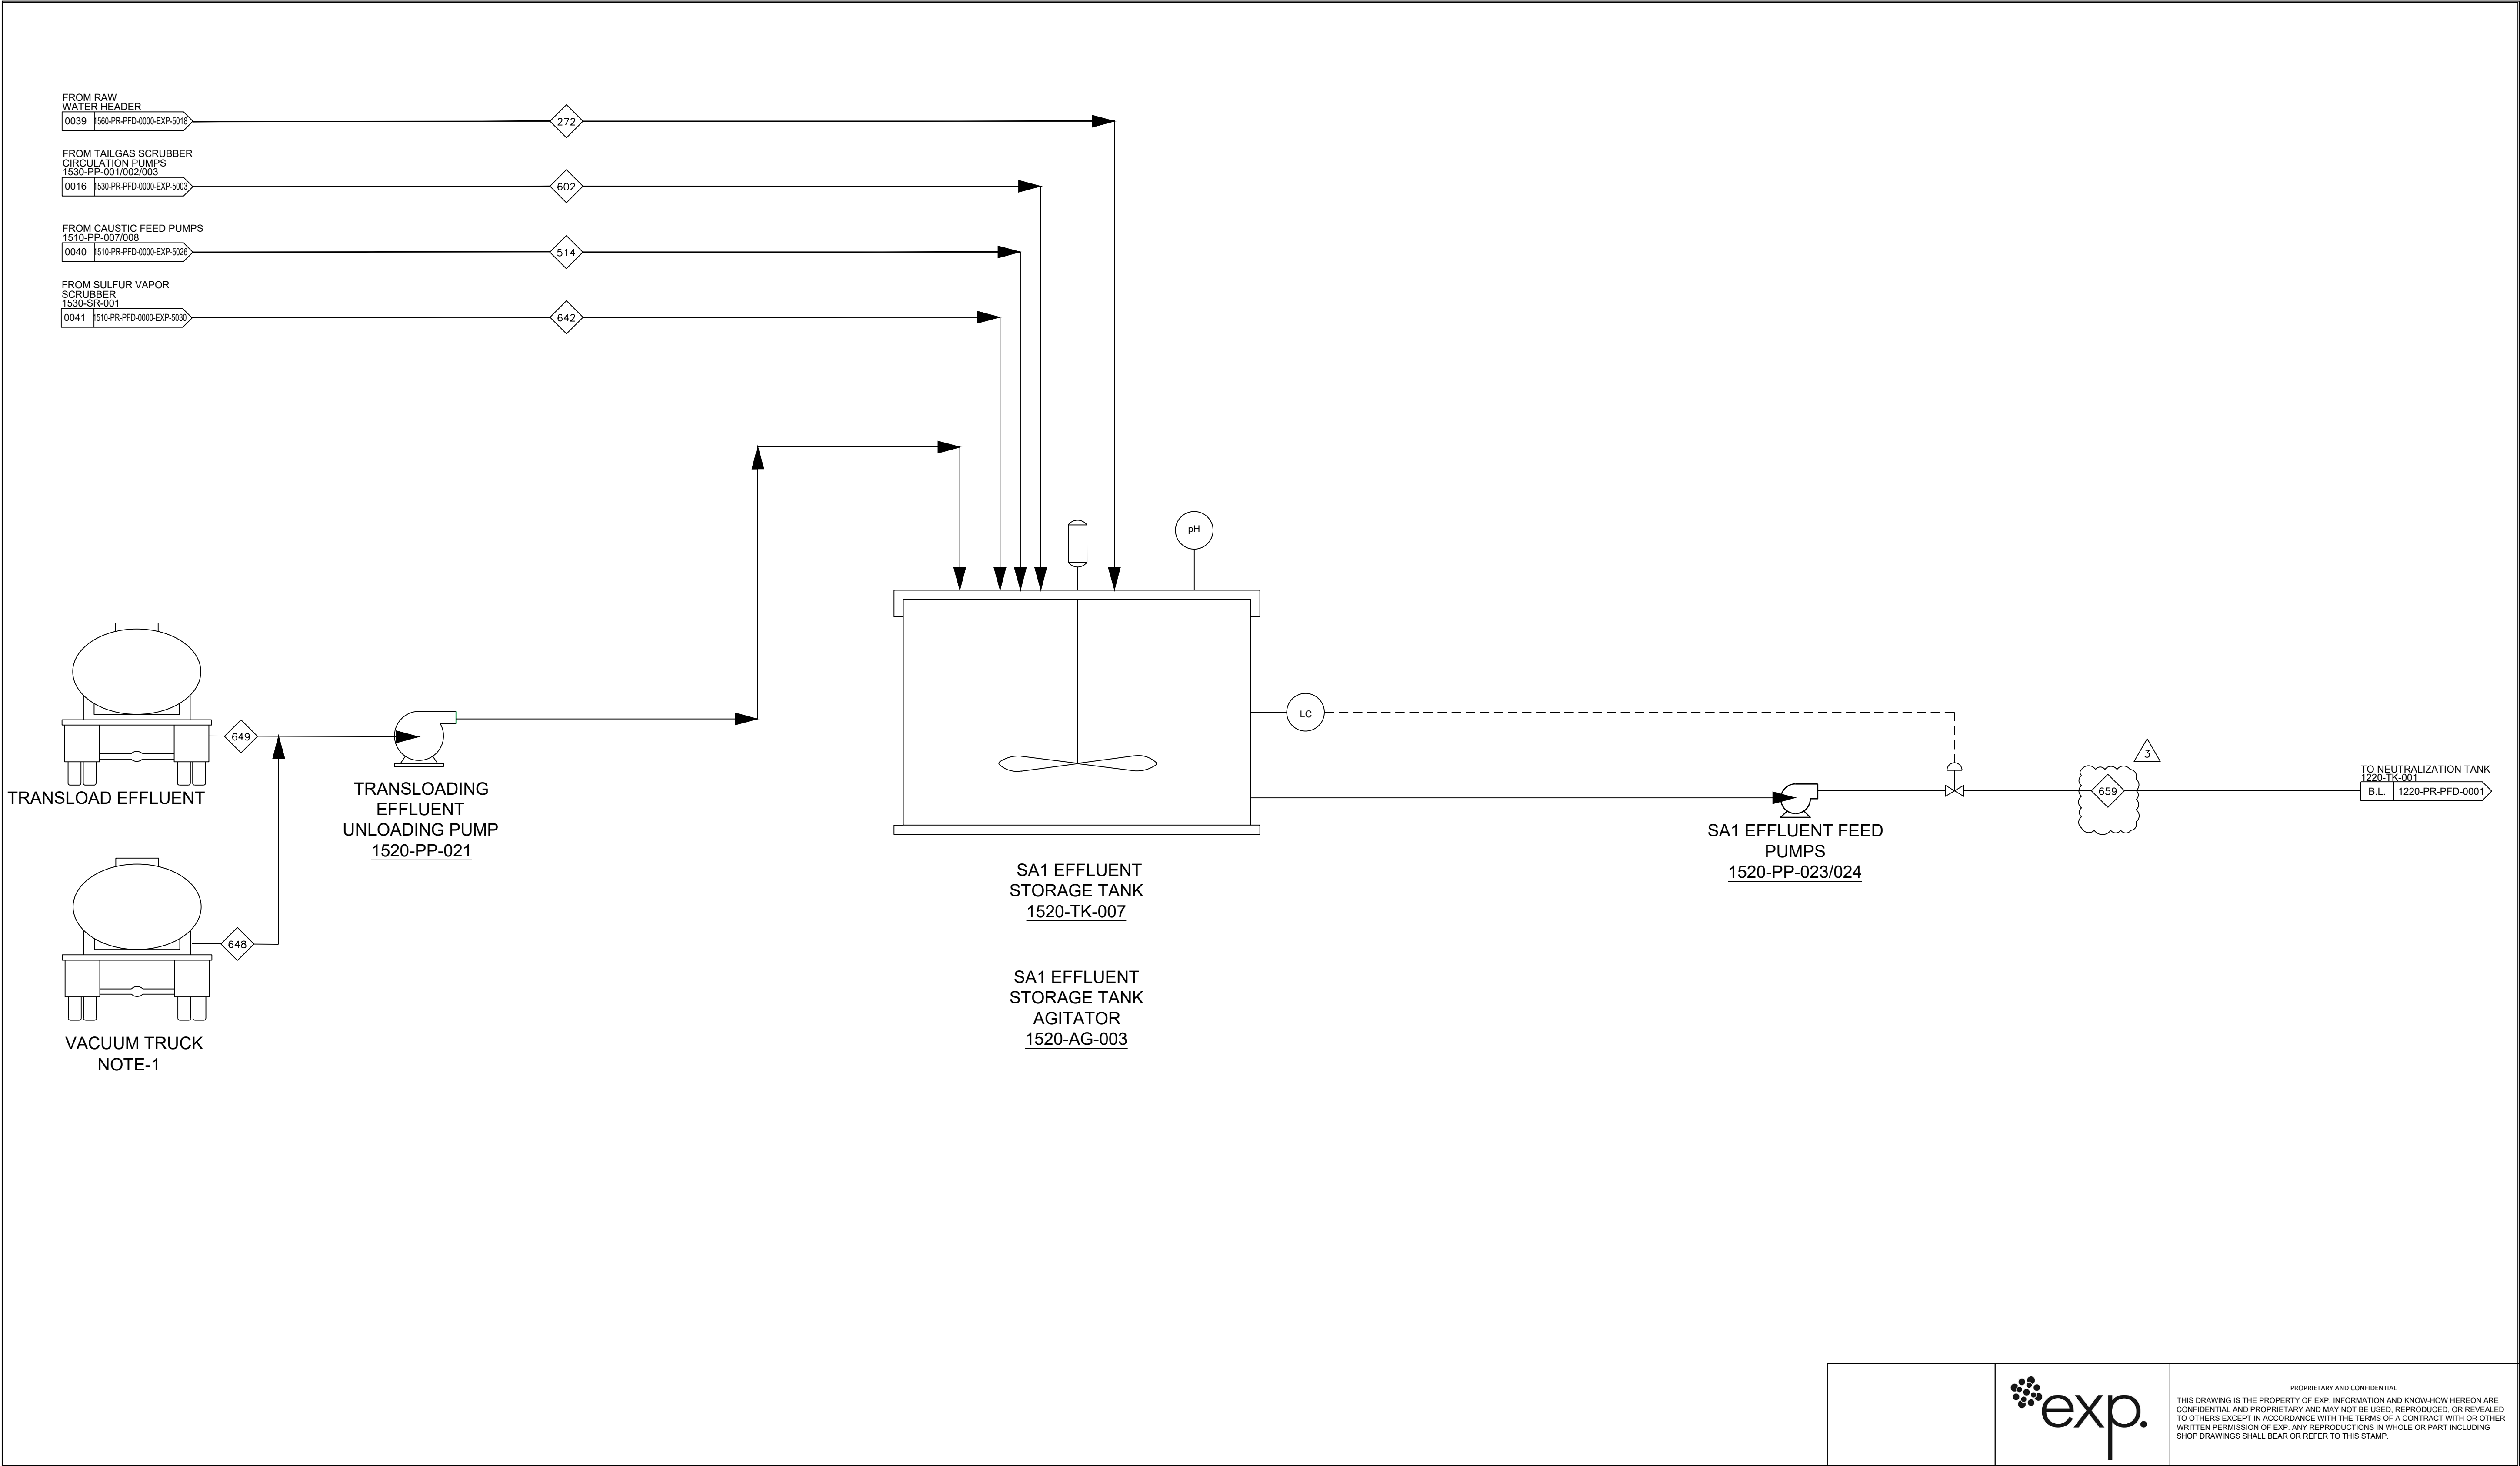

1500-PR-HMB-0000-EXP-5101	MATERIAL BALANCE - DESIGN CASE 105 RATE - UTILITIES
1500-PR-HMB-0000-EXP-5100	MATERIAL BALANCE - DESIGN CASE 100 RATE - UTILITIES
DWG. NO.	TITLE
REFERENCES	

NOTES:	
1. EFFLUENT UNLOADING PUMP DESIGNED TO UNLOAD TRANSLOAD EFFLUENT AND VACUUM TRUCK EFFLUENT.	
2. DELETED	
3.	

3	REVISED STREAM NUMBER				2024-10-25
2	REVISED STREAM NUMBER AND OPC DESTINATION	AS	BA	TV	2024-09-23
1	REVISED EFFLUENT UNLOADING PUMP CONFIGURATION	SJ	BA	TV	2024-08-01
0	ISSUED FOR DESIGN	RM	BA	TV	2024-01-16
B	ISSUED FOR CLIENT REVIEW	RM	BA	TV	2023-12-11
A	ISSUED FOR REVIEW	RM	BA		2023-11-23
NO.	DESCRIPTION	BY	CHK	APP'D	DATE
REVISIONS					

SEAL
EXP t: +1 713 439 3600 f: +1 713 963 9085 exp.com

NOTICE
Property of Lithium Americas Corp (LAC). The contents of this drawing are confidential and proprietary to Lithium Americas Corp. The information contained in this drawing may not be distributed, duplicated, or modified without prior written permission from Lithium Americas Corp. All rights reserved.

SCALE	N/A	SIZE	D
DRAWN BY	R. MASANI	DATE	2024-01-16
CHECKED BY	D. BIRD	DATE	2024-01-16
ENGINEERED BY	B. AFELSKIE	DATE	2024-01-16
APPROVED BY	T. VAN DAELE	DATE	2024-01-16

PROPRIETARY AND CONFIDENTIAL


THIS DRAWING IS THE PROPERTY OF EXP. INFORMATION AND KNOW-HOW HEREON ARE CONFIDENTIAL AND PROPRIETARY AND MAY NOT BE USED, REPRODUCED, OR REVEALED TO OTHERS EXCEPT IN ACCORDANCE WITH THE TERMS OF A CONTRACT WITH OR OTHER WRITTEN PERMISSION OF EXP. ANY REPRODUCTIONS IN WHOLE OR PART INCLUDING SHOP DRAWINGS SHALL BEAR OR REFER TO THIS STAMP.

THACKER PASS PROJECT
HUMBOLDT COUNTY, NV

PROJ No. HOU-23001048-A1	REV
DRAWING No. 1520-PR-PFD-0000-EXP-5028	3

TITLE

2,250MTPD SA1 - DCDA
PROCESS FLOW DIAGRAM
EFFLUENT TANK

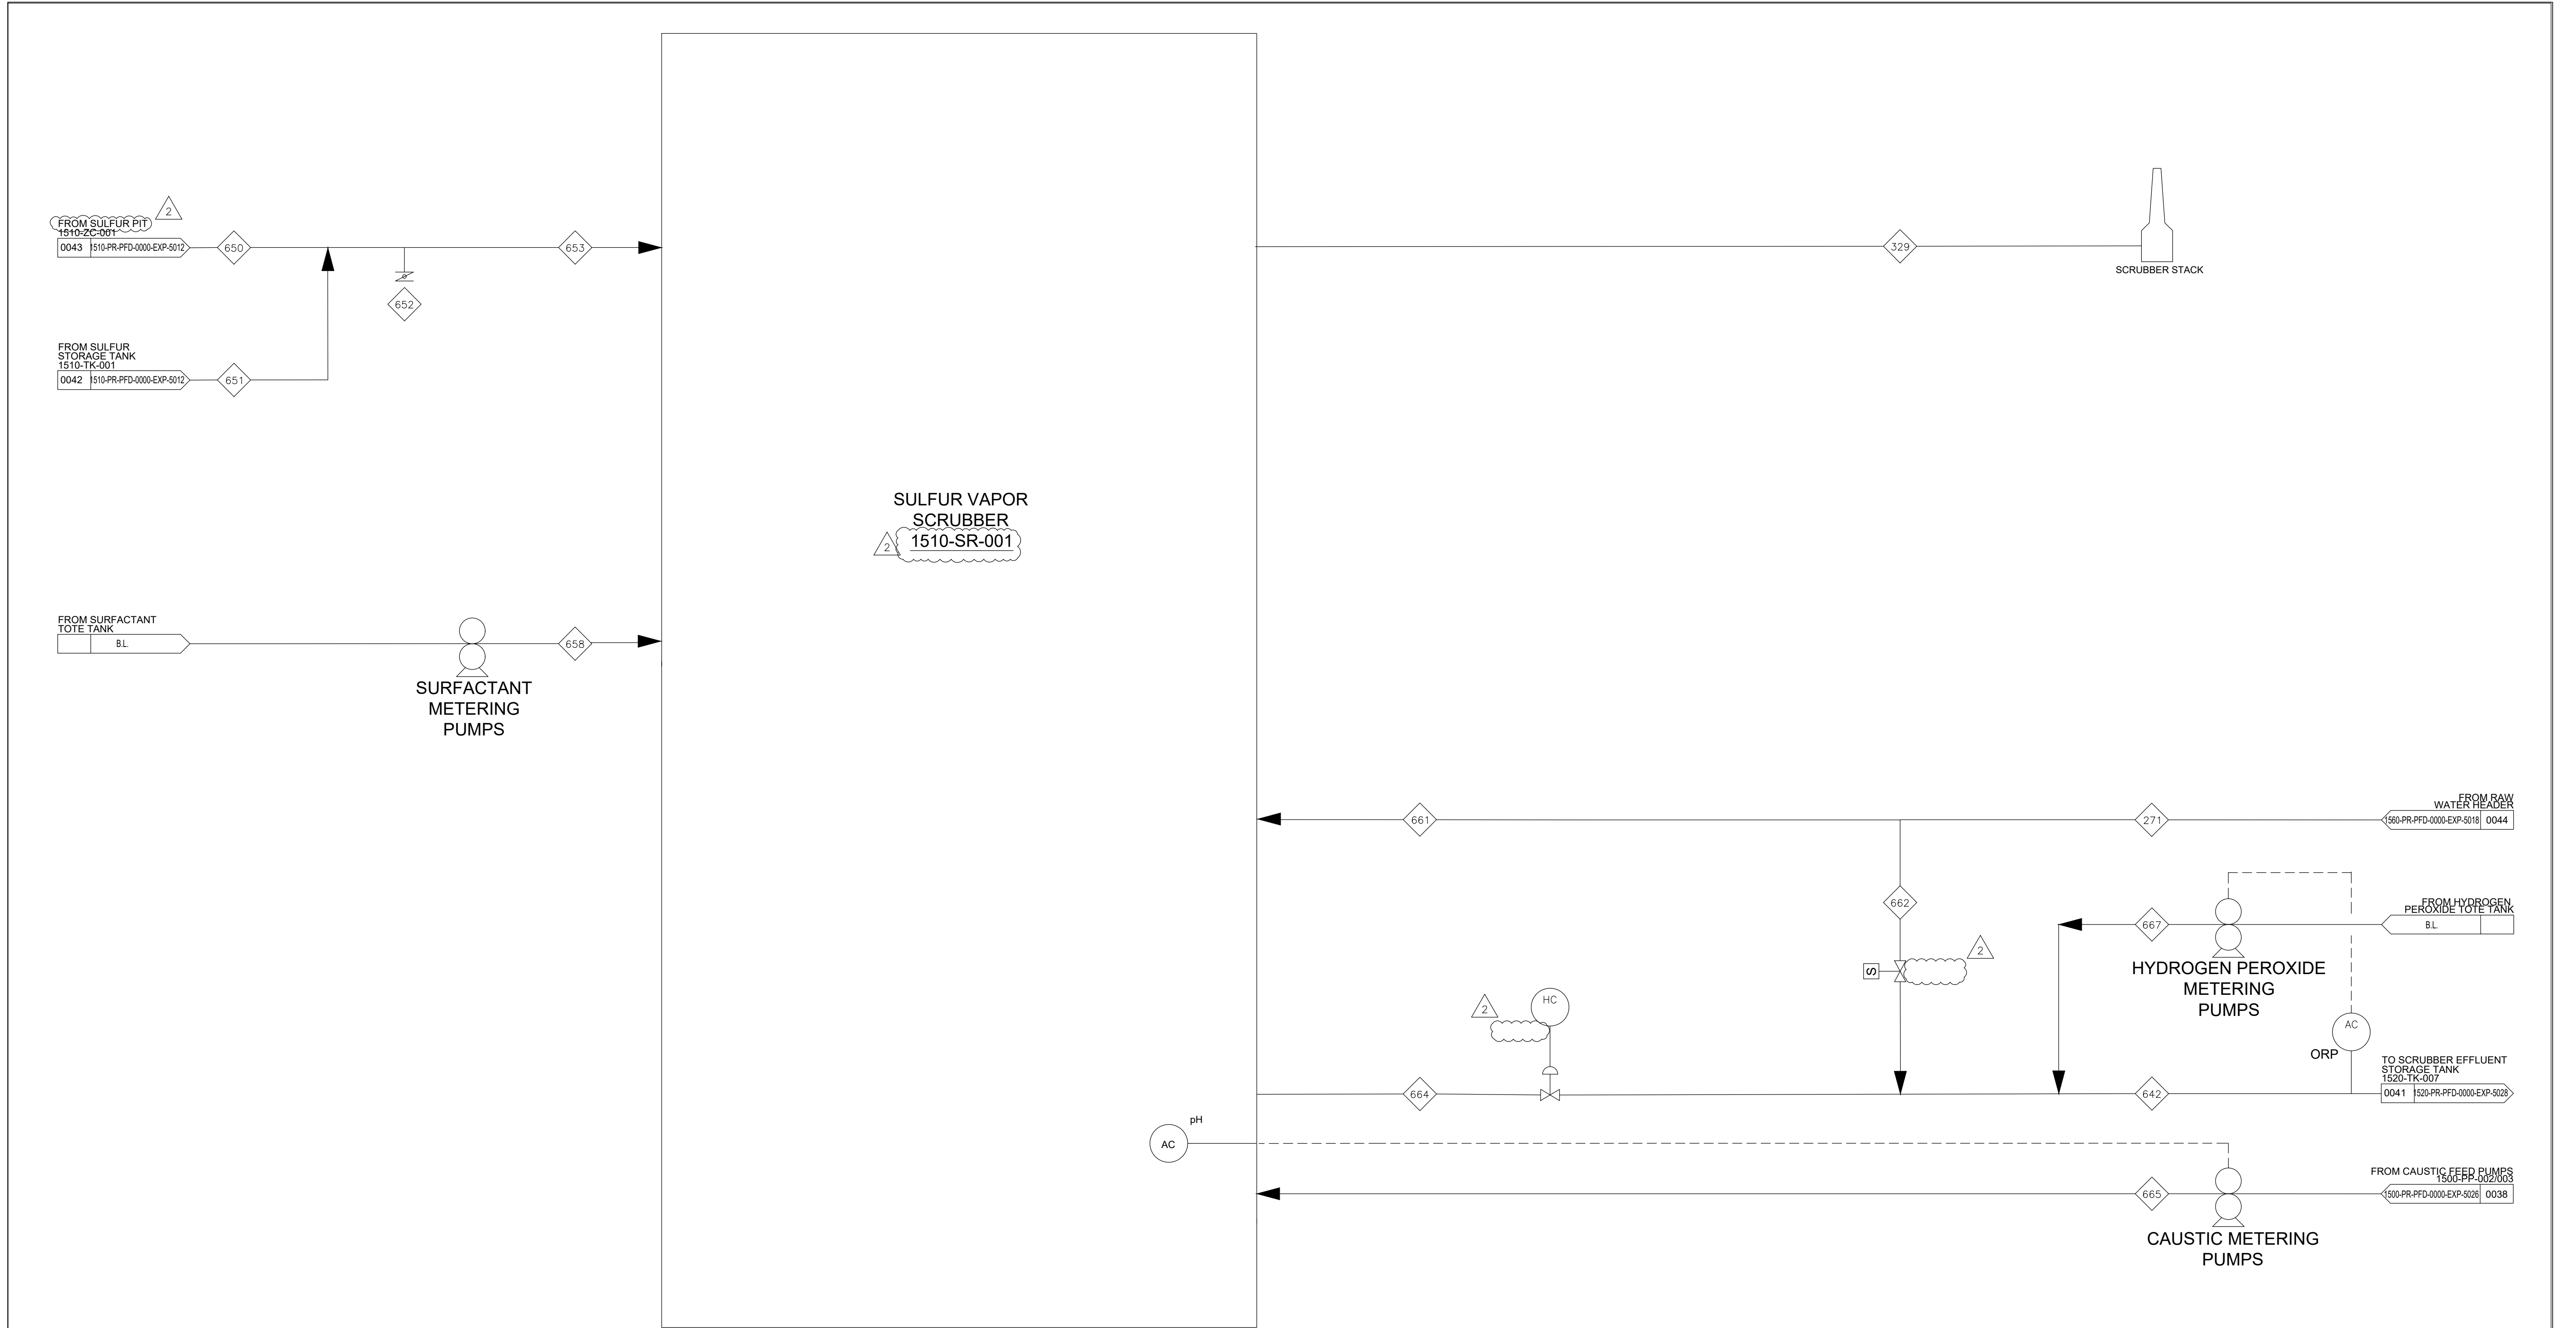[illegible]

DRAWING PLOTTED:



STREAM NUMBER		350	351	352	353
COMPONENT		Propane Gas	Propane Gas	Propane Gas	Propane Gas
FLOW	LB/H	7.828	3.407	4.195	226
FLOW	SCFM	1.122	489	601	32
NORMAL PRESSURE	PSIG	50	50	50	50
NORMAL TEMPERATURE	°F	40	40	40	40

NOTES:

1. PEAK FLOWRATE PROVIDED. AUX BOILER NOT REQUIRED DURING NORMAL OPERATION
2. PEAK FLOWRATE PROVIDED. START-UP BURNER IS INSTALLED IN SULFUR FURNACE DURING STARTUP ONLY. REMOVED DURING NORMAL OPERATION.

SEAL

NOTICE
Property of Lithium Americas Corp (LAC). The contents of this drawing are confidential and proprietary to Lithium Americas Corp. The information contained in this drawing may not be distributed, duplicated, or modified without prior written permission from Lithium Americas Corp. All rights reserved

SCALE	SIZE
N/A	D
DRAWN BY	DATE
R.MASANI	2024-01-16
CHECKED BY	DATE
D.BIRD	2024-01-16
ENGINEERED BY	DATE
B.AFELSKIE	2024-01-16
APPROVED BY	DATE
T.VAN.DAELE	2024-01-16



PROPRIETARY AND CONFIDENTIAL
THIS DRAWING IS THE PROPERTY OF EXP. INFORMATION AND KNOW-HOW HEREON ARE CONFIDENTIAL AND PROPRIETARY AND MAY NOT BE USED, REPRODUCED, OR REVEALED TO OTHERS EXCEPT IN ACCORDANCE WITH THE TERMS OF A CONTRACT WITH OR OTHER WRITTEN PERMISSION OF EXP. ANY REPRODUCTIONS IN WHOLE OR PART INCLUDING SHOP DRAWINGS SHALL BEAR OR REFER TO THIS STAMP.

LithiumAmericas
2,250MTPD SA1 - DCDA
PROCESS FLOW DIAGRAM
PROPANE

THACKER PASS
PROJECT
HUMBOLDT COUNTY, NV

PROJ No. HOU-23001048-A1
DRAWING No.
1500-PR-PFD-0000-EXP-5032

REV
2

DWG. NO.	TITLE
1500-PR-SPC-0000-EXP-5005	PROCESS SPECIFICATION - PROPANE SUPPLY SYSTEM
REFERENCES	

NO.	DESCRIPTION	BY	CHK	APP'D	DATE
2	REVISED PROPANE FLOW RATES				2024-10-25
1	REVISED OFF PAGE CONNECTOR	SJ	BA	TV	2024-08-01
0	ISSUED FOR DESIGN	RM	BA	TV	2024-01-16
B	ISSUED FOR CLIENT REVIEW	RM	BA	TV	2023-12-11
A	ISSUED FOR REVIEW	RM	BA		2023-11-23
REVISIONS					

EXP
t: +1.713.439.3600 | f: +1.713.963.9085
exp.com